


# PLANOS ULTIMATE - CONSTRUCCIÓN DE LA MAQUETA

Documento exclusivo para cortar, perforar, ensamblar y terminar la estructura física

## PROJECT DOMUS · maqueta cruda acotada · sin instalaciones

GEMELO DIGITAL v4 · MAQUETA CRUDA · SIN INSTALACIONES

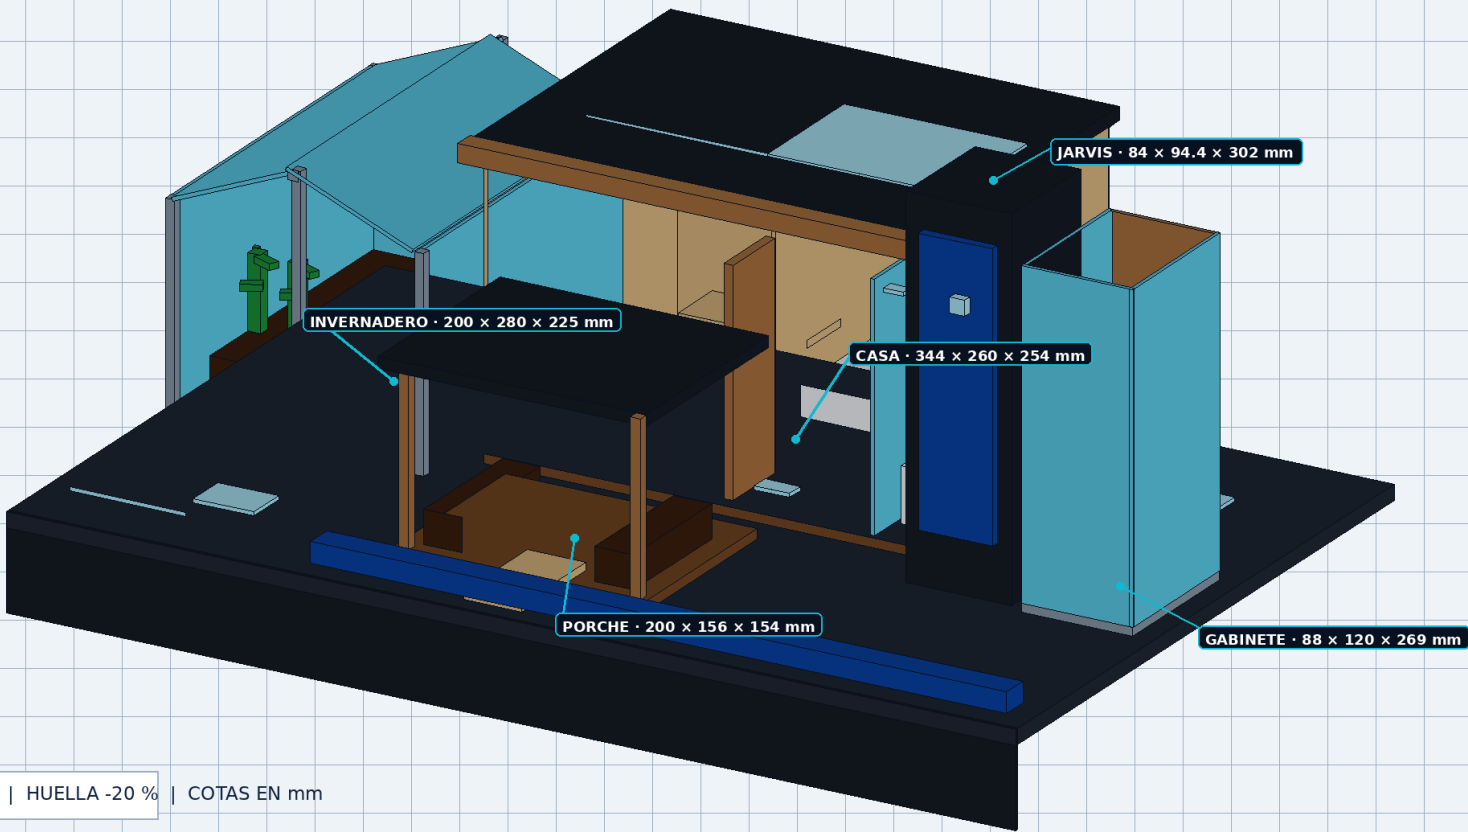

### QUÉ CONSTRUYE EL EQUIPO

- Base, faldón y tapas removibles.
- Casa abierta, mobiliario y tabiques.
- Porche, pasarela, jardineras e invernadero.
- Bancales/macetas con forros removibles.
- Carcasas vacías de Jarvis y gabinete.
- Pasamuros cerrados y marcas futuras.


### QUÉ NO CONSTRUYE NI INSTALA

- No sensores, ESP32, relés o fuente.
- No cables, conectores ni soldaduras.
- No bomba, tubos ni depósito definitivo.
- No luces ni paneles solares reales.
- No abrir huecos de sensor sin medir la pieza.

BASE FINAL: 800 × 520 mm - REDUCCIÓN UNIFORME AL 80 % DEL DISEÑO ORIGINAL

# IMPLANTACIÓN GENERAL Y EJES DE MONTAJE

Origen X0/Y0 en la esquina frontal izquierda; el faldón PROJECT DOMUS define el frente

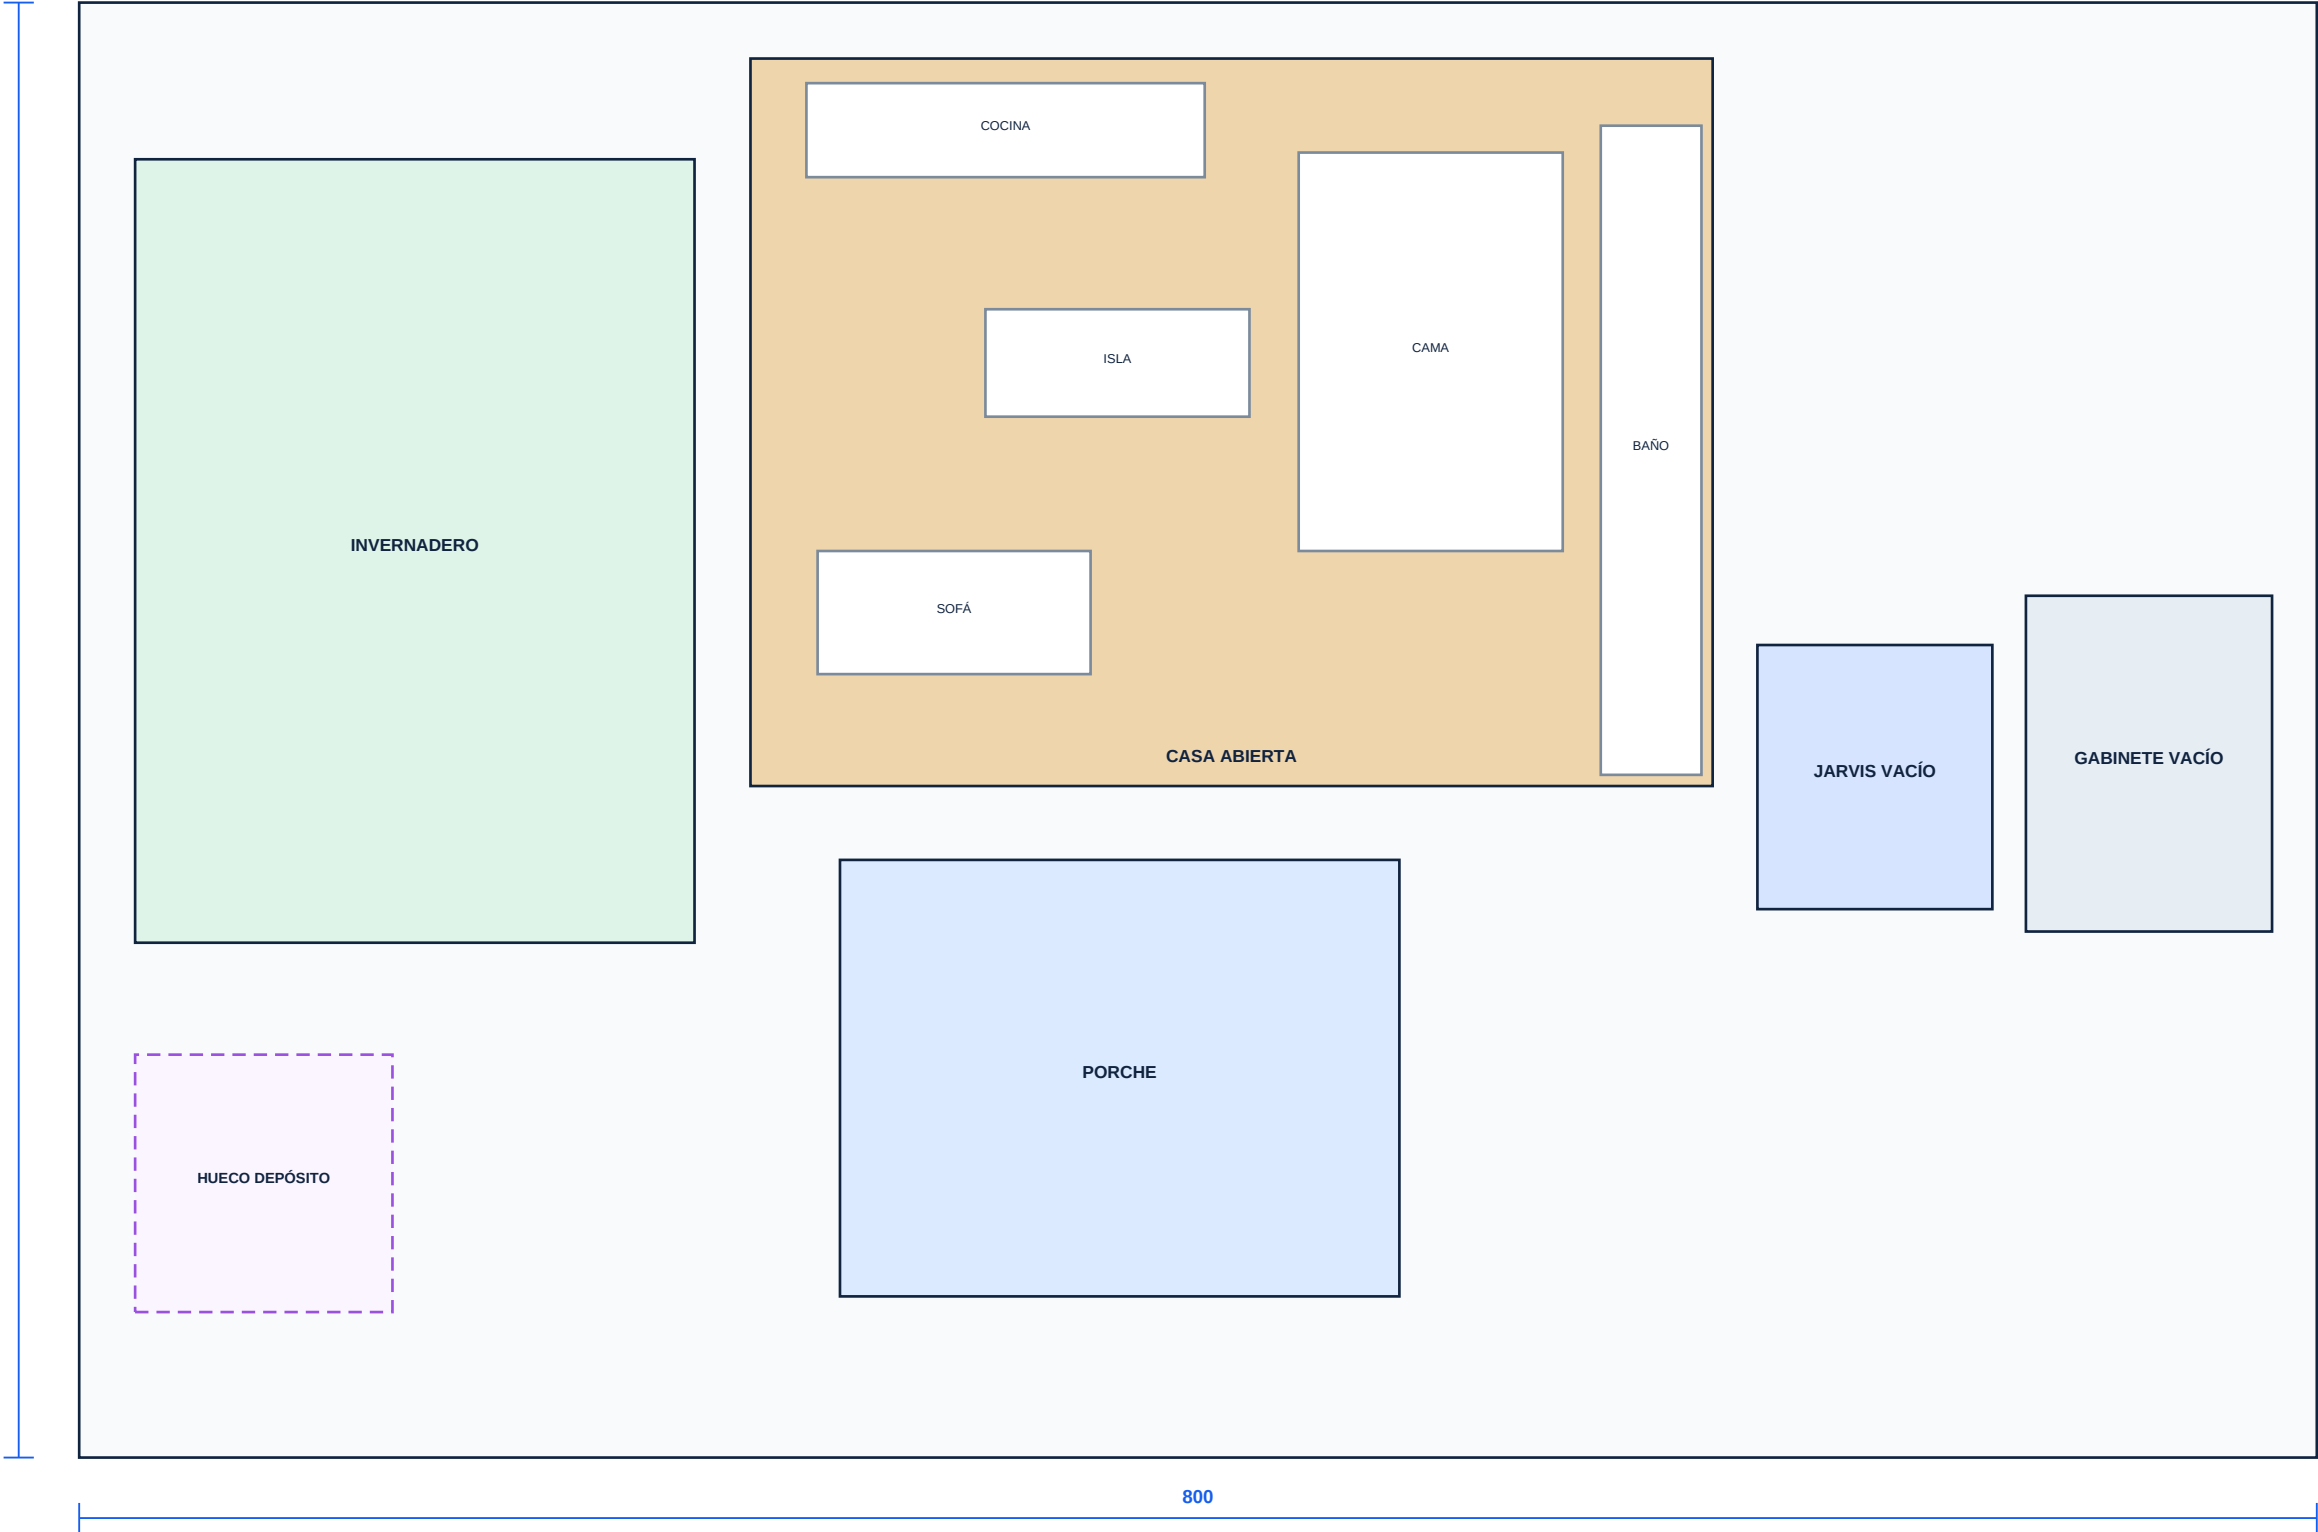

## COORDENADAS

Invernadero: X20 / Y184

Casa: X240 / Y240

Porche: X272 / Y57.6

Jarvis: X600 / Y196

Gabinete: X696 / Y188

Depósito futuro: X20 / Y52

## REGLAS

1. Marcar todo antes de pegar.
2. Presentar módulos en seco.
3. No recentrar ningún módulo.
4. Tolerancia de posición:  $\pm 0.5$ .
5. Sólido = pieza; punteado = hueco.

## ALTURAS DE PROYECTO

Casa: Z superior 254


Invernadero: Z superior 225

Jarvis: Z superior 302

Gabinete: Z superior 269

# BASE, FALDÓN, CANAL VACÍO Y PASAMUROS

Todas las perforaciones de esta lámina son mecánicas; se entregan sin cables

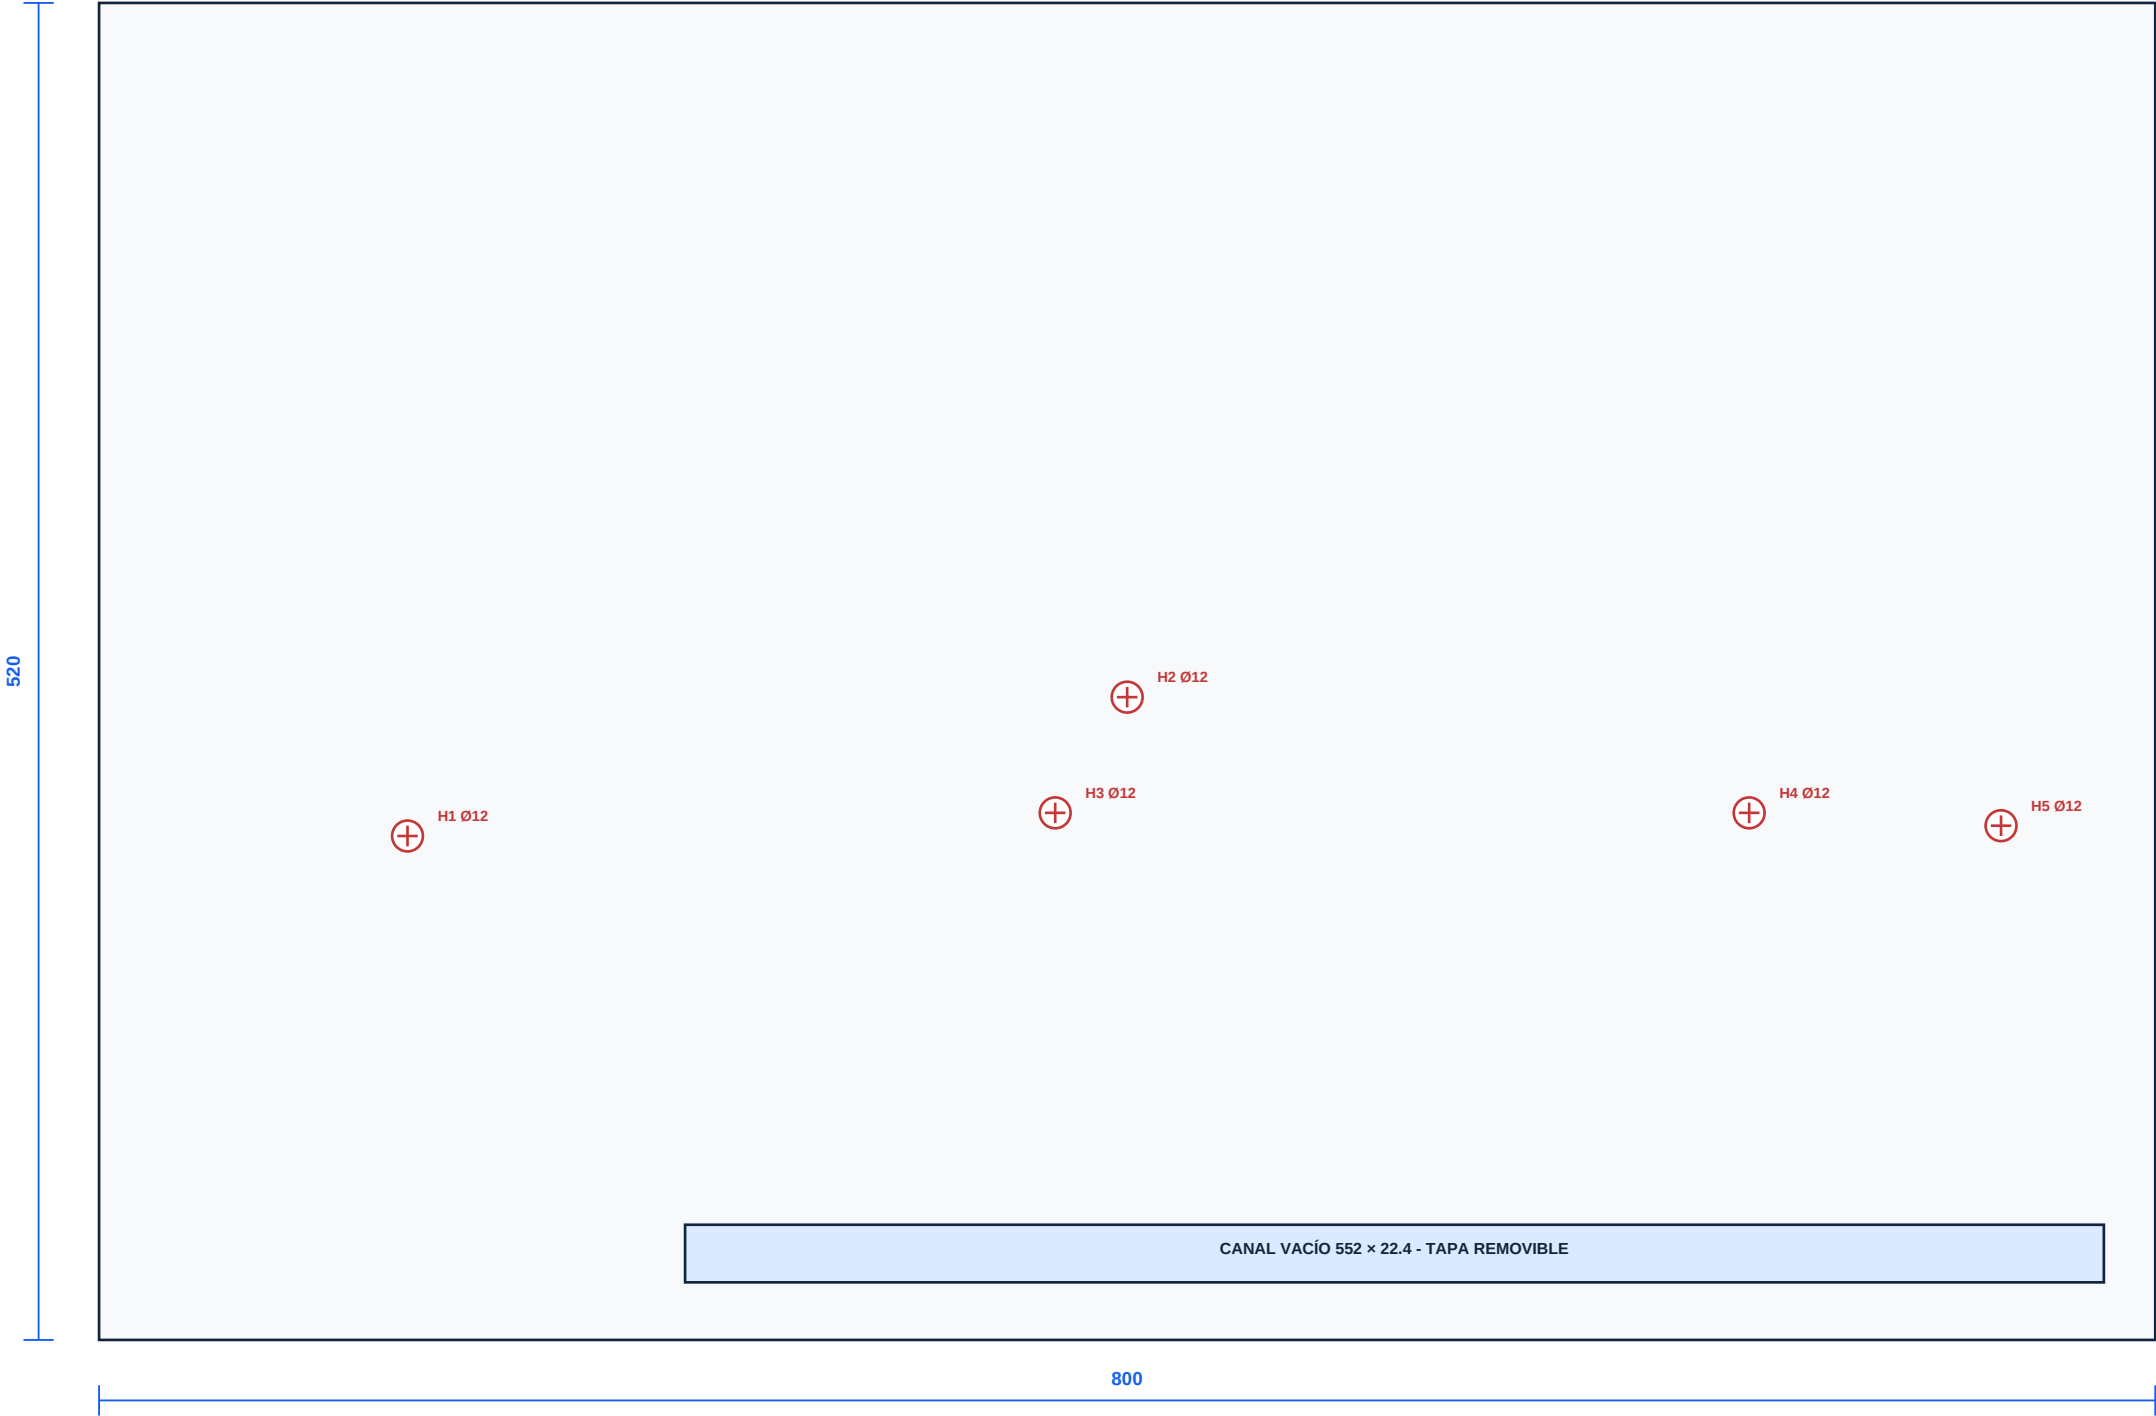

## DESPIECE BASE

B-01 MDF 12: 800 × 520

B-02 Faldón 3: 800 × 75

B-03 Tapa canal 3: 552 × 22.4

Faldón: borde superior a Z12

Borde inferior a Z-63

Profundidad real del faldón: 3

## PERFORACIÓN

H1-H5: Ø12 pasante.

Taladrar con madera apoyada.

Avellanar: NO.

Colocar tapón removible Ø12.

No introducir cable ni conector.

Desbarbar ambas caras.

## ACABADO


Sellar MDF antes de pintar.

Negro mate; no pintar zonas de adhesión.

Comprobar planitud máxima 1 mm.

CASA ABIERTA - PLANTA, MUROS Y TECHO

Huella 344 × 260; frente completamente abierto; altura interior 225

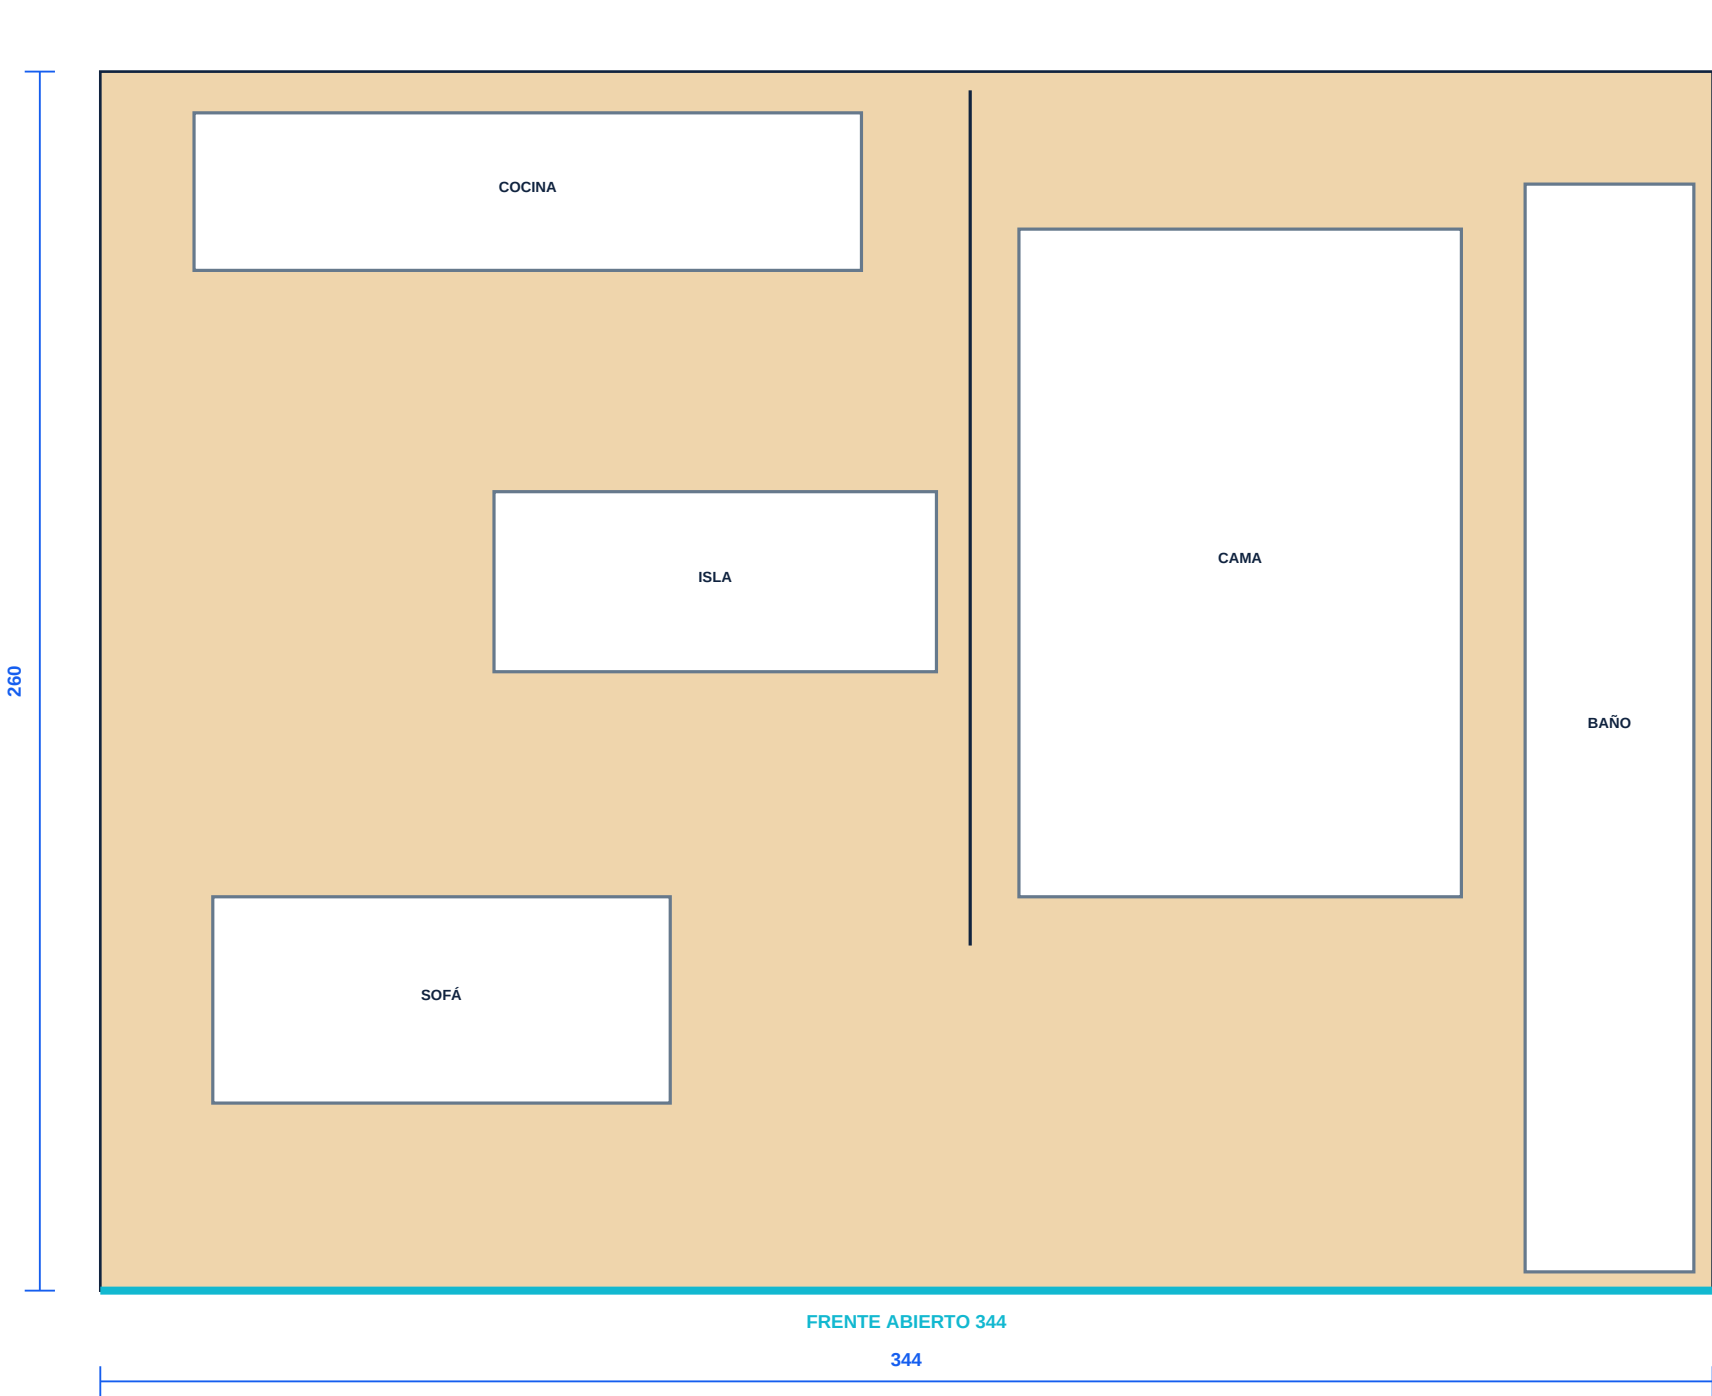

PIEZAS Y PERFORACIONES

Piso: 344 × 260 × 3 sobre bastidor 7 × 7.

Posterior: 344 × 225 × 3.

Laterales: 260 × 225 × 3 (2).

Techo removible: 356.8 × 272.8 × 3.

Hatch posterior: 70 × 40; reutilizar recorte.

4 alojamientos de imán Ø8 × 4 prof., a 8 de cada borde.

No abrir perforaciones de sensor en paredes.

# INTERIOR DE LA CASA - MOBILIARIO Y TABIQUES

Las piezas interiores son parte visual de la maqueta; pueden fabricarse como volúmenes huecos

| Código | Elemento           | Cantidad | Medida exterior   | Material / criterio          |
|--------|--------------------|----------|-------------------|------------------------------|
| F-01   | Mueble bajo cocina | 1        | 142.4 × 33.6 × 68 | Plywood 3; caja hueca        |
| F-02   | Encimera cocina    | 1        | 147.2 × 38.4 × 7  | Madera 3 + separadores       |
| F-03   | Refrigerador       | 1        | 38.4 × 52.8 × 138 | Foamboard 3; volumen hueco   |
| F-04   | Isla               | 1        | 94.4 × 38.4 × 70  | Plywood 3; tapa 102.4 × 46.4 |
| F-05   | Sofá               | 1        | 97.6 × 44 × 52    | Foamboard + tela/EVA         |
| F-06   | Mesa sala          | 1        | 56 × 38.4 × 31    | Madera 2-3                   |
| F-07   | Cama               | 1        | 94.4 × 142.4 × 61 | Base 37 + colchón 24         |
| F-08   | Mesa de noche      | 1        | 30.4 × 30.4 × 42  | Madera 2-3                   |
| F-09   | Baño esquemático   | 1        | 36 × 232 de zona  | Acrílico/blanco; sin tubería |
| F-10   | Tabique dormitorio | 1        | 182.4 × 188 × 3   | Plywood 3; removible         |

## POSICIONES LOCALES DESDE CASA X0/Y0



- Cocina: X20 / Y217.6
- Isla: X84 / Y132
- Sofá: X24 / Y40
- Cama: X196 / Y84
- Baño: X304 / Y4
- Tabique: X185.6 / Y73.6
- Puerta: ancho 57.6; alto 174
- Mantener pasillo central mínimo 24.

## CRITERIO DE CONSTRUCCIÓN

- Se permite simplificar tiradores y textiles.
- No cambiar huellas ni posiciones.
- Ningún mueble debe ocultar H-02.
- Baño decorativo: no conectar agua.
- Presentar en seco antes de fijar.
- Tolerancia de mobiliario: ±1 mm.

PORCHE, PASARELA Y JARDINERAS

Plataforma 200 × 156; cubierta 212.8 × 168; cubierta inferior en Z154

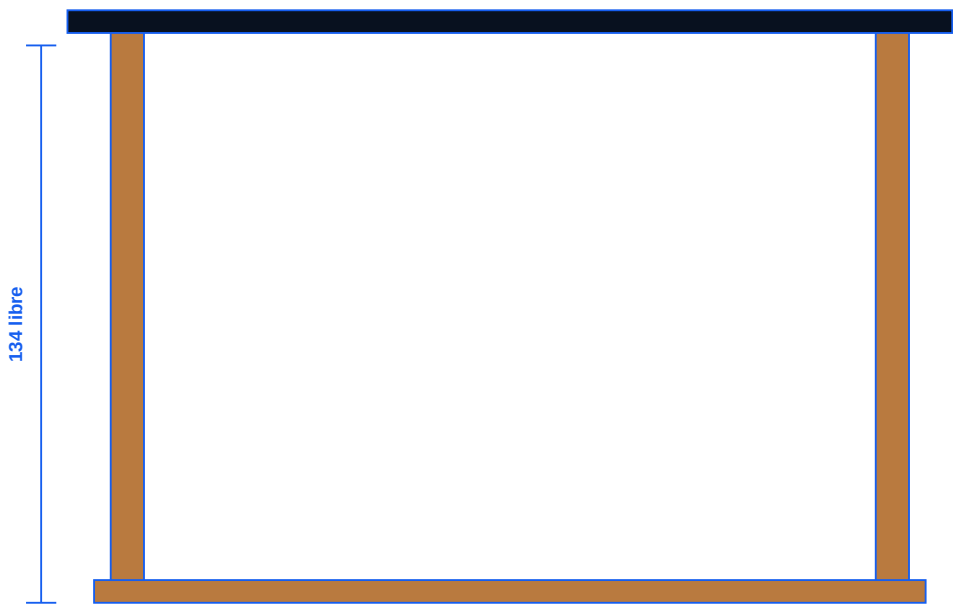
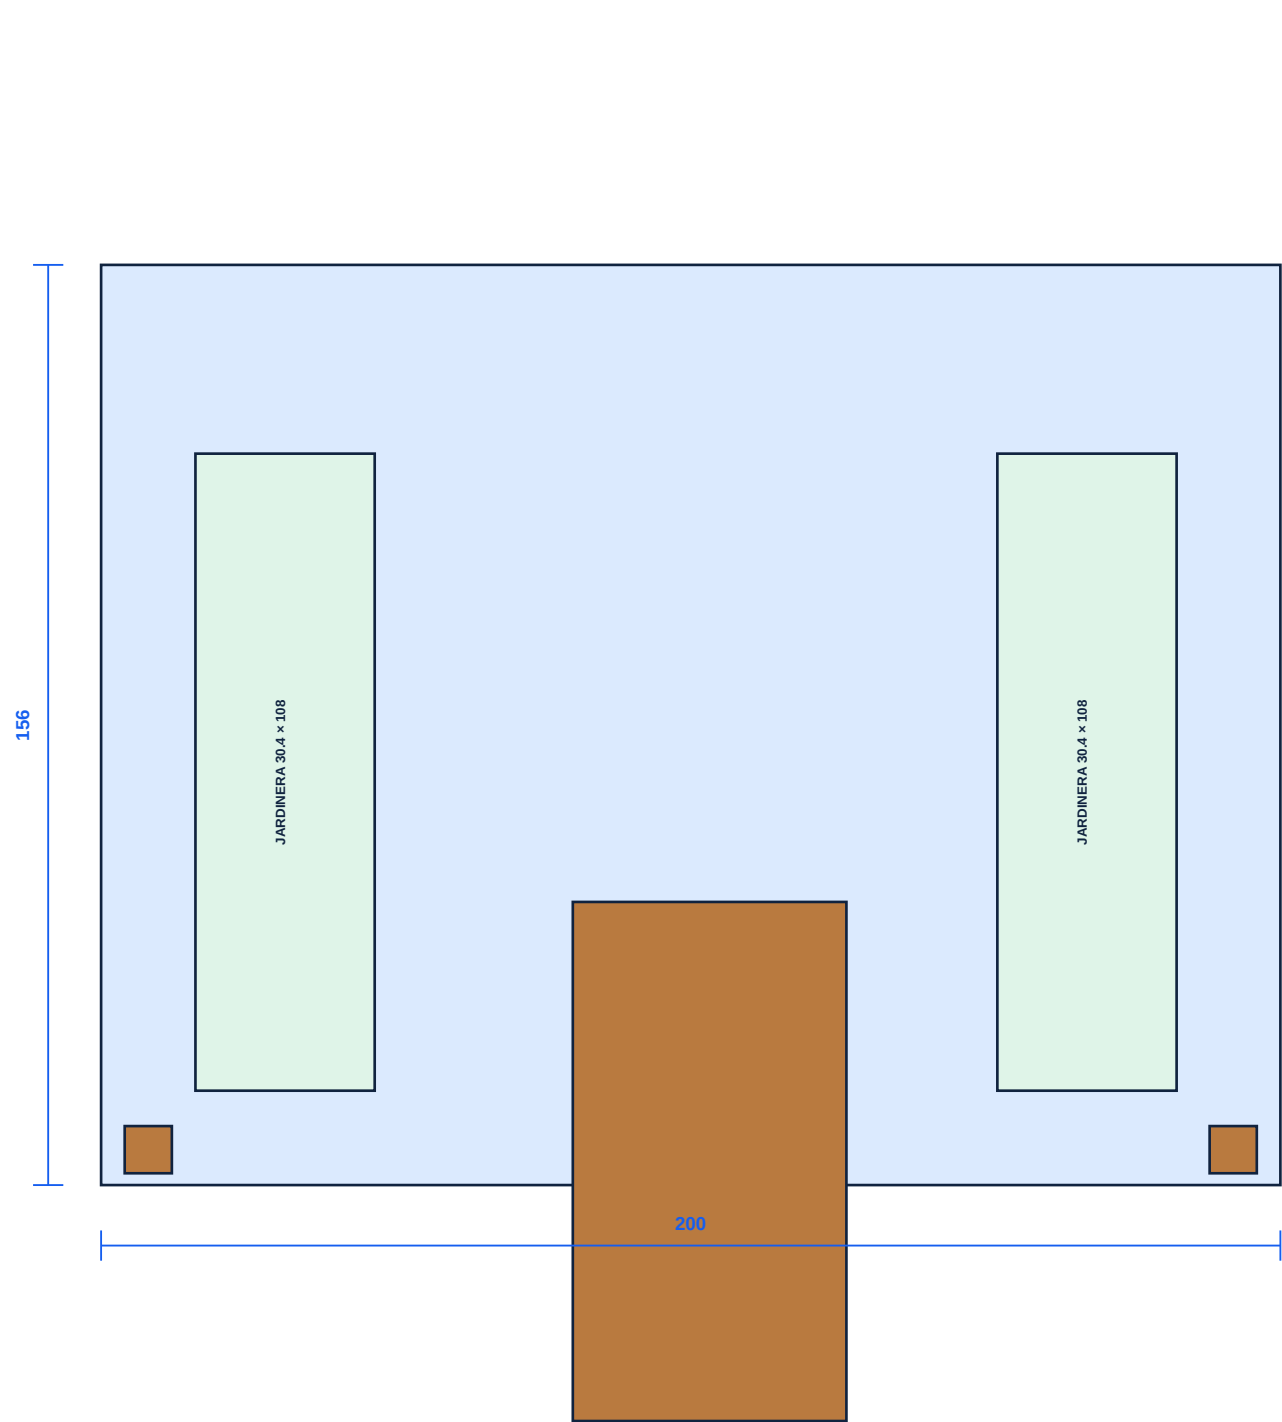


JARDINERAS (2 UNIDADES)

- Exterior: 30.4 × 108 × 26; PVC 2 mm.
- Interior útil: 26.4 × 104 × 22.
- Altura máxima de tierra: 18; dejar 4 libres.
- Forro PET removable; no pegar al cajón.
- Marcar 2 centros Ø3 en el forro, sin perforar aún.
- Volumen de tierra recomendado: 45-50 mL cada una.

# INVERNADERO Y BANCALES PARA TIERRA

Huella 200 × 280; cumbrera Z225; paneles transparentes sin sensores ni tuberías

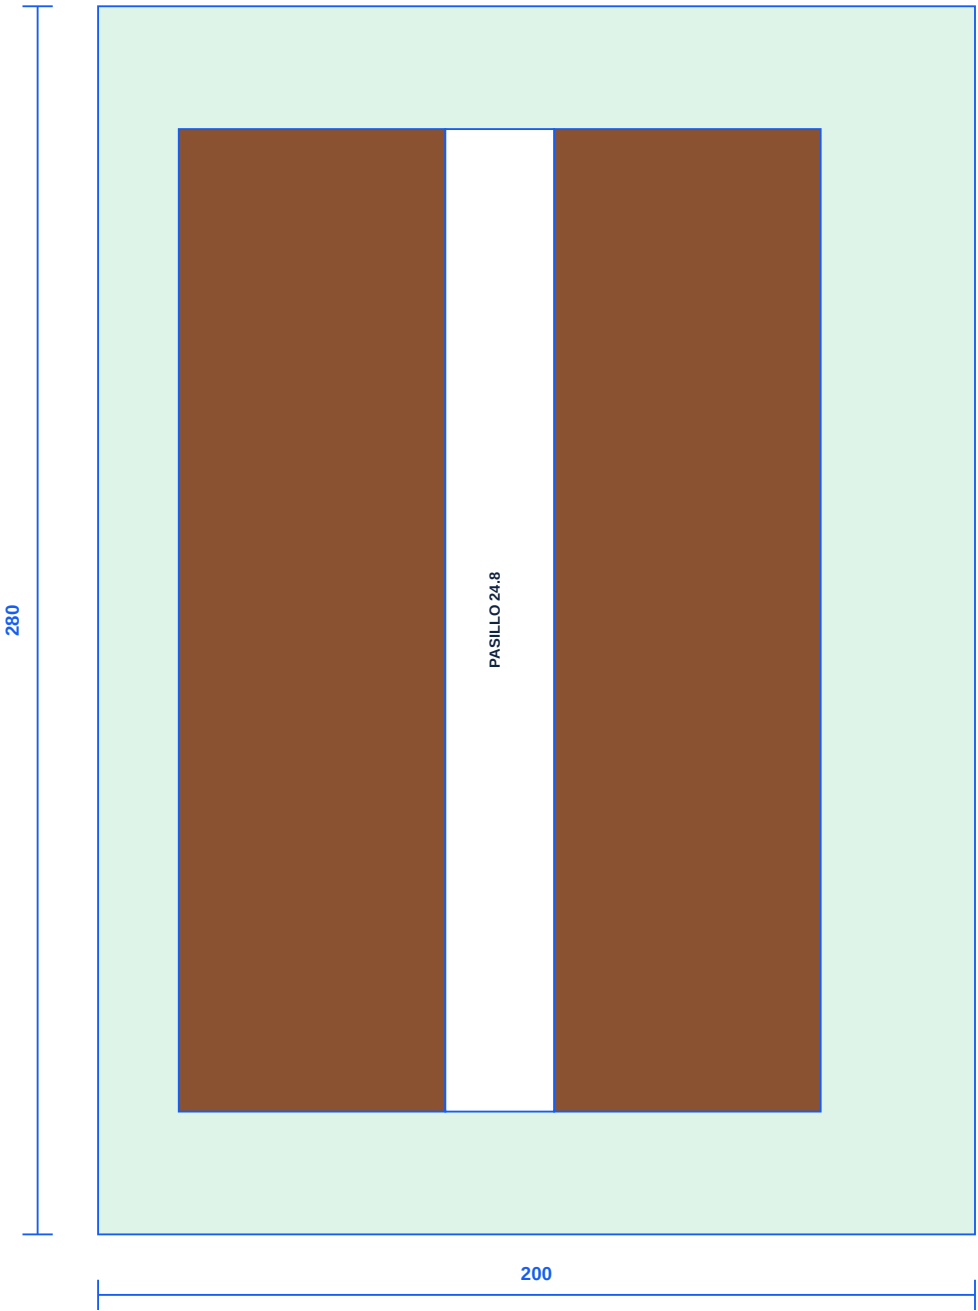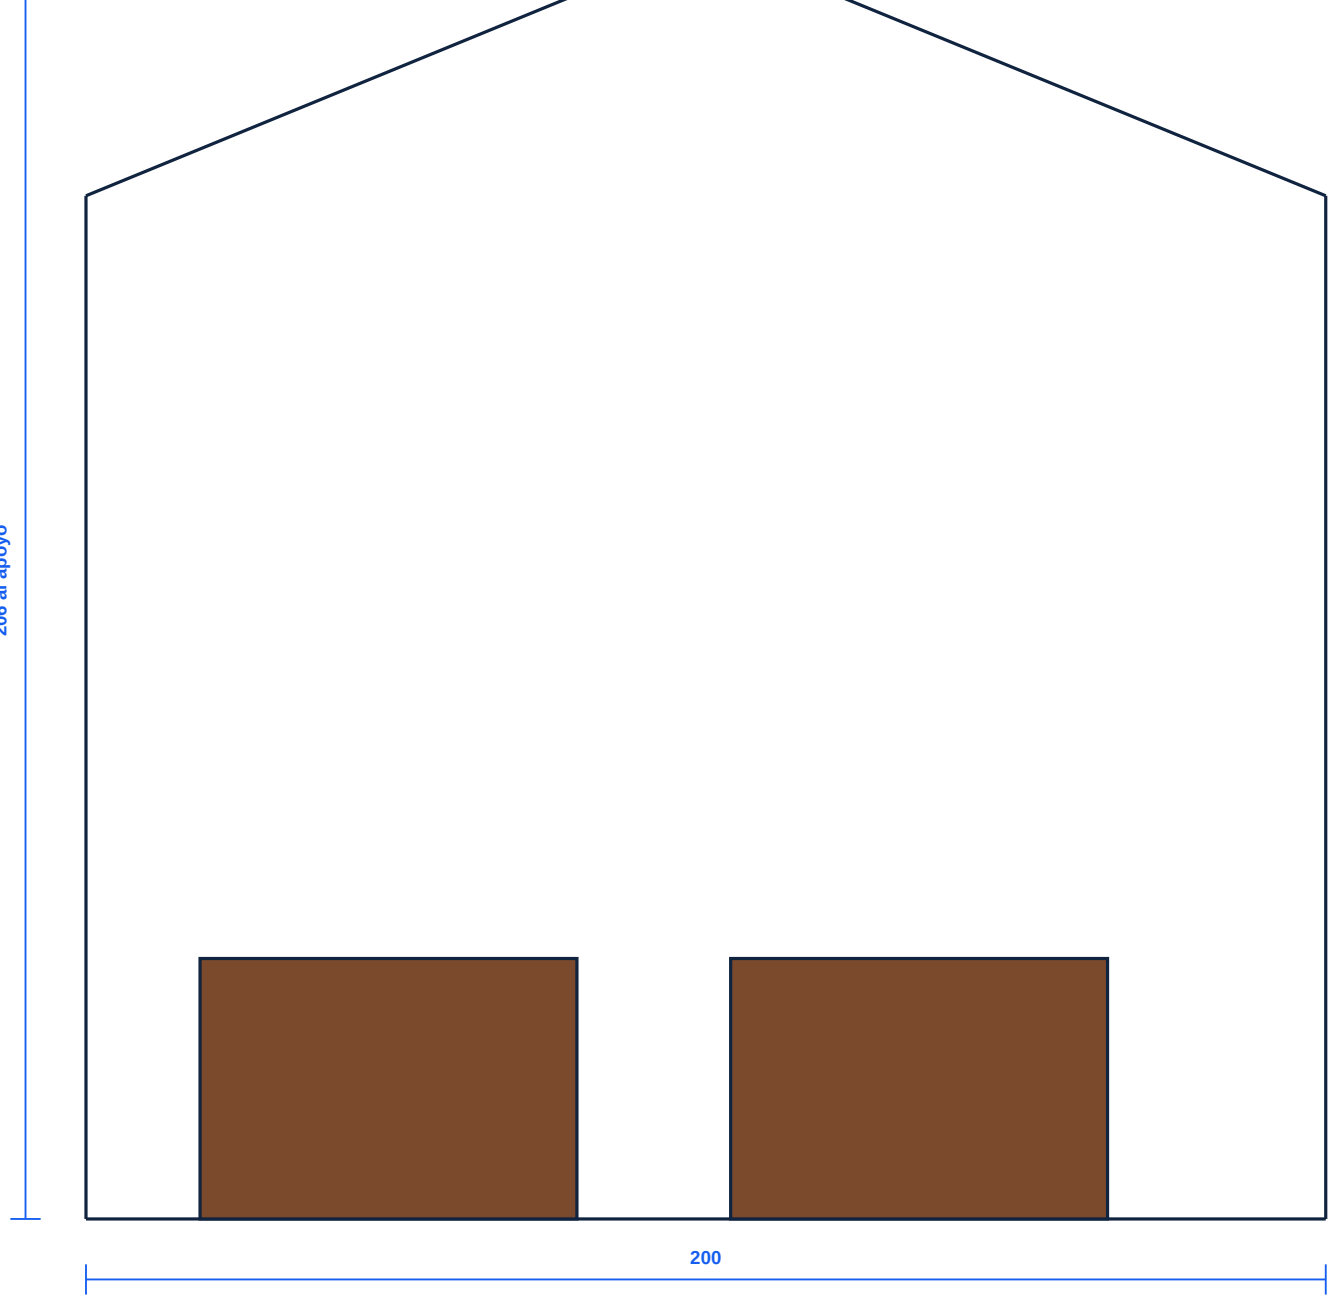

DESPIECE

- Base: 200 × 280 × 3
- Laterales: 280 × 165 × 1.5 (2)
- Posterior: 200 × 165 × 1.5
- Techo: 280 × 108.1 × 1.5 (2)
- Pendiente: 22.3°
- Postes ext.: 7 × 7 × 165 (4)
- Postes cumbrera: 7 × 7 × 206 (2)
- Viga: 8 × 8 × 280

BANCAL / MACETA (2)

- Exterior: 60.8 × 224 × 42
- Pared/fondo: PVC 2
- Interior: 56.8 × 220 × 38
- Tierra máxima: 30 de alto
- Volumen aprox.: 0.375 L cada uno
- Inserto removible: 16 × 16
- Marcar Ø8 para futura sonda
- No perforar hasta medir sensor

Diagrama de un panel de control vertical. El panel es un rectángulo azul con tres secciones rectangulares blancas con bordes de puntos rojos. Las secciones están etiquetadas como 'PANTALLA' (superior), 'ALTAVOZ' (intermedia) y 'BOTÓN' (inferior). A la izquierda del panel, una línea vertical azul indica una altura de 290. Debajo del panel, una línea horizontal azul indica una anchura de 84.

Altura de proyecto desde Z0: 302.

Altura de proyecto desde Z0: 269.

Proteger el acrílico durante el armado y retirar la película solo al final.

# PERFORACIONES, INSERTOS Y PIEZAS REMOVIBLES

Diferenciar claramente: TALADRAR AHORA, MARCAR SOLAMENTE y NO PERFORAR

| ID   | Ubicación              | Centro / referencia     | Acción            | Entrega                               |
|------|------------------------|-------------------------|-------------------|---------------------------------------|
| H-01 | Base bajo invernadero  | X 120 / Y 196           | Ø12 pasante       | Colocar tapón; sin cable              |
| H-02 | Base bajo casa         | X 400 / Y 250           | Ø12 pasante       | Colocar tapón; sin cable              |
| H-03 | Base bajo porche       | X 372 / Y 205           | Ø12 pasante       | Colocar tapón; sin cable              |
| H-04 | Base bajo Jarvis       | X 642 / Y 205           | Ø12 pasante       | Colocar tapón; sin cable              |
| H-05 | Base bajo gabinete     | X 740 / Y 200           | Ø12 pasante       | Colocar tapón; sin cable              |
| H-06 | Techo casa, 4 esquinas | A 8 mm de cada borde    | Ø8 × 4 prof.      | Alojamiento de imanes                 |
| H-07 | Hatch muro posterior   | Centrado; borde inf. 15 | 70 × 40           | Recorte reutilizado como tapa         |
| H-08 | Insertos de bancal     | Local 30 / 112          | 16 × 16 removible | Marcar Ø8; no abrir hasta medir sonda |

## TALADRAR AHORA

- H-01 a H-05: Ø12 pasante.
- H-06: alojamientos Ø8 × 4 prof.
- H-07: hatch 70 × 40.
- Desbarbar, sellar y probar tapas.
- Entregar H-01 a H-05 con tapón.
- No pasar ningún cable.

## MARCAR SOLAMENTE

- Ø8 en insertos de bancales.
- Zonas de pantalla/micrófono/altavoz.
- Puntos M2 del gabinete.
- Centros de drenaje Ø3 en forros.
- Usar línea fina morada o grabado suave.

## NO PERFORAR

Paneles transparentes del invernadero, muebles, baño ni fachadas visibles.  
Toda apertura variable se confirma con el componente físico.

# MATERIALES, LISTA DE CORTE Y CONTROL DE CALIDAD

Comprar por espesor; verificar el calibre real con pie de rey antes de cortar

| ID   | Material                        | Espesor/sección | Cantidad                   | Uso                                  |
|------|---------------------------------|-----------------|----------------------------|--------------------------------------|
| M-01 | MDF                             | 12 mm           | 1 pieza 800 × 520          | Base estructural                     |
| M-02 | Plywood/MDF                     | 3 mm            | 2 láminas 600 × 900 aprox. | Casa, cubiertas, pisos y faldón      |
| M-03 | Acrílico transparente           | 1.5 mm          | 1 lámina 600 × 900         | Invernadero                          |
| M-04 | Acrílico transparente           | 3 mm            | 1 lámina 300 × 450         | Gabinete y tapas removibles          |
| M-05 | Listón cuadrado                 | 7 × 7 mm        | 2.5 m                      | Bastidores e invernadero             |
| M-06 | Listón cuadrado                 | 8 × 8 mm        | 1.2 m                      | Porche y cumbrera                    |
| M-07 | PVC espumado                    | 2 mm            | 1 lámina A3                | Bancales y jardineras                |
| M-08 | PET/acetato flexible            | 0.5 mm          | 4 recortes                 | Forros impermeables removibles       |
| M-09 | Imán neodimio                   | Ø8 × 4 mm       | 4 pares                    | Techo removible de la casa           |
| M-10 | Pasamuros/tapón                 | Ø12 mm          | 5 unidades                 | Accesos futuros, entregados cerrados |
| M-11 | Adhesivo PVA + cemento acrílico | -               | Según consumo              | Uniones estructurales                |
| M-12 | Pintura/sellador                | -               | Negro mate + protector     | Base, cantos y madera                |

## CONTROL DE CALIDAD ANTES DE ENTREGAR

- Base 800 × 520, plana y escuadrada.
- Módulos en las coordenadas U-01.
- Casa de una planta y frente abierto.
- Techo, hatch y frentes removibles.
- Bancales y jardineras con forro removible.
- Invernadero sin grietas ni tensión.
- H-01 a H-05 cerrados con tapones.
- Marcas futuras visibles pero sin cortar.
- Jarvis y gabinete completamente vacíos.
- Sin sensores, cables, bomba o conexiones.

## TOLERANCIAS

Corte estructural ±0.5 - Mobiliario ±1.0 - Perforaciones ±0.3 - Escuadra máxima 0.5 por 300 - Planitud base máxima 1.0

Orden obligatorio: marcar → presentar en seco → perforar → sellar cantos → pegar → probar removibles → pintar → inspeccionar.

## ARCHIVOS COMPLEMENTARIOS

Lista de corte completa: lista\_corte\_ultimate.csv  
Perforaciones: perforaciones\_y\_accesos.csv  
Materiales: materiales\_ultimate.csv