


JUEGO DE PLANOS TÉCNICOS

A3 apaisado · cotas en milímetros · maqueta educativa de baja tensión

PROJECT DOMUS · maqueta de una planta · sistema 100 % local

GEMELO DIGITAL v3 · 100 % LOCAL · 5 V DC

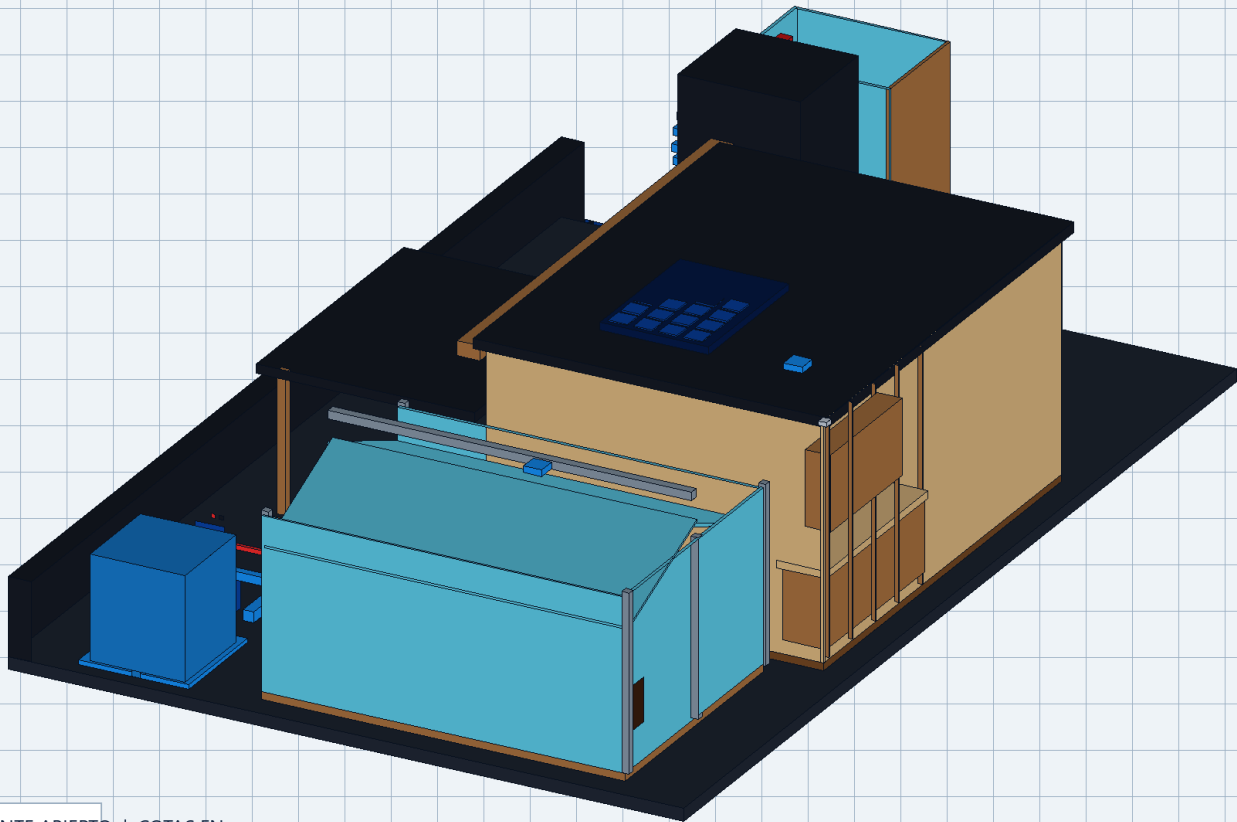

BASE 1000 × 650 mm | FRENTE ABIERTO | COTAS EN mm

ÍNDICE VISUAL


- 01 Implantación y planta general
- 02 Elevaciones y sección
- 03 Baja tensión y control
- 04 Agua y riego seguro
- 05 Explosión, montaje y corte

DATOS PRINCIPALES

Base 1000 × 650 × 12 · 5 V DC · local · sin radio ni nube

IMPLANTACIÓN Y PLANTA GENERAL

Ejes, huellas y recorridos principales; el frente de exposición queda abajo

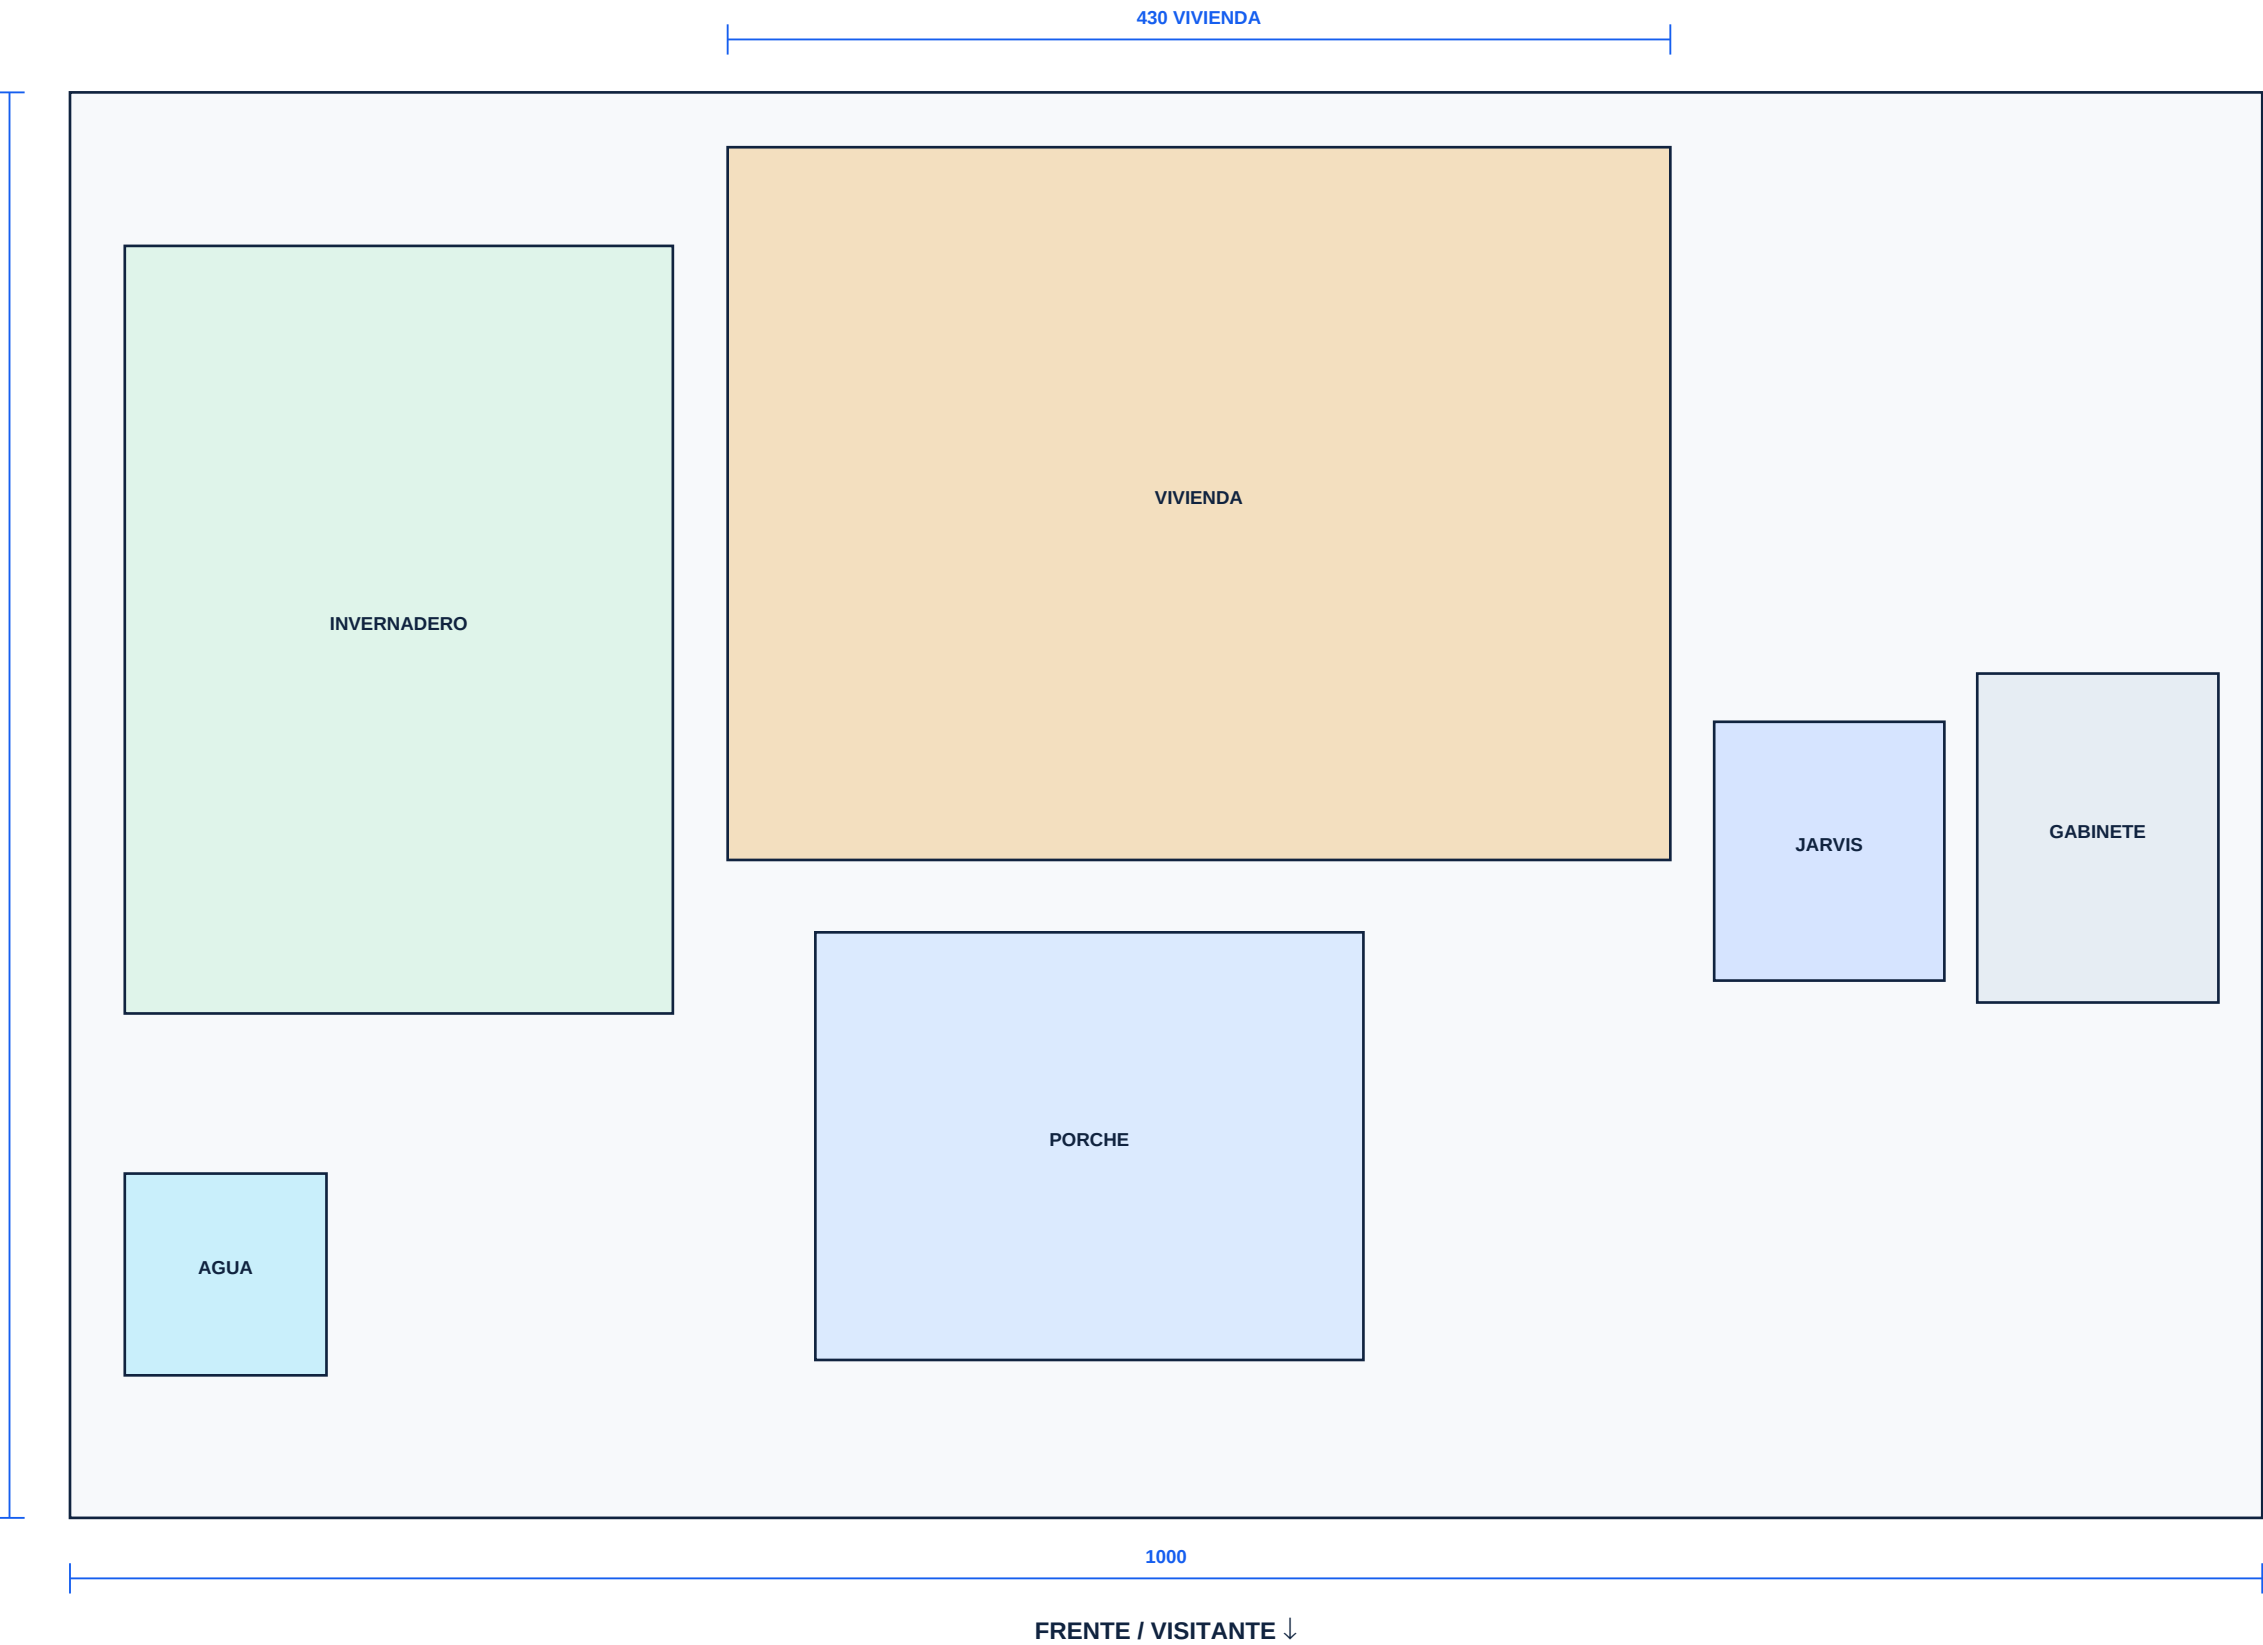

HUELLAS

- Invernadero 250 × 350 × 225
- Casa 430 × 325 × 254 total
- Porche 250 × 195 × 154
- Jarvis 105 × 118 × 302
- Gabinete 110 × 150 × 269
- Depósito 92 × 92 × 100

SEPARACIÓN FUNCIONAL

- Agua al extremo izquierdo.
- Control al extremo derecho.
- Canaleta inferior con tapa.
- Techo y gabinete removibles.

Alturas totales y lectura del interior abierto


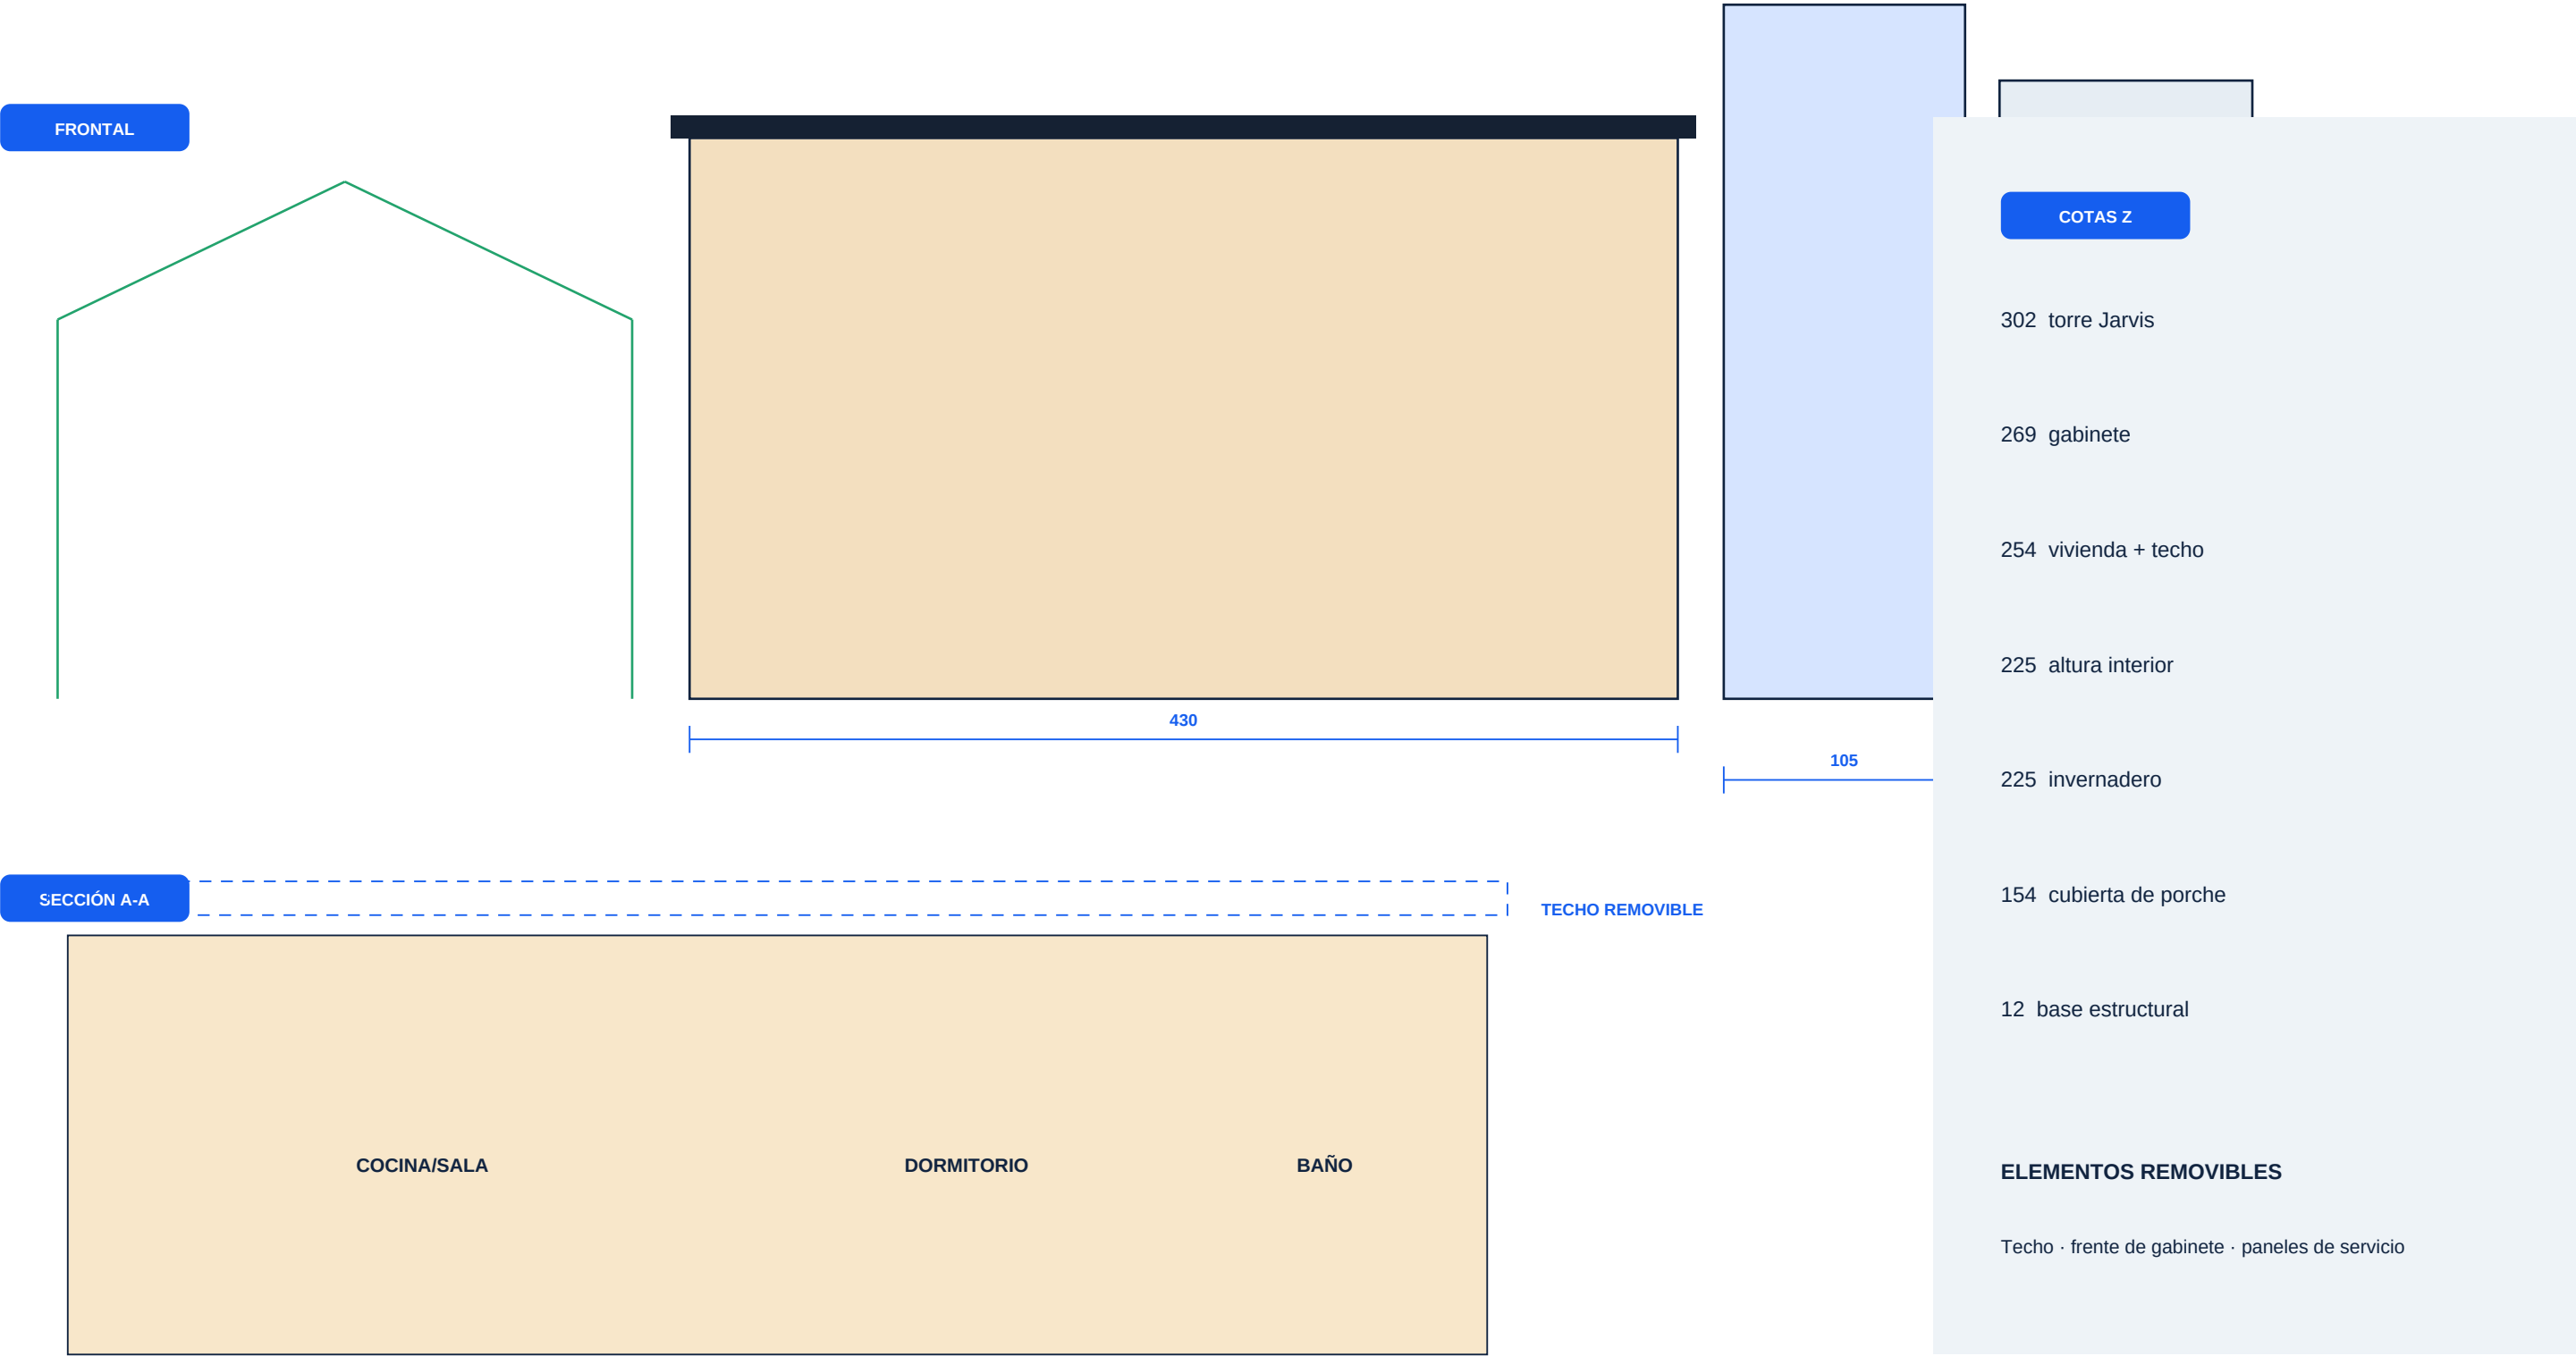


Diagrama funcional; usar la tabla de cableado validada para GPIO concretos



Depósito separado, lectura de nivel y bloqueo de bomba

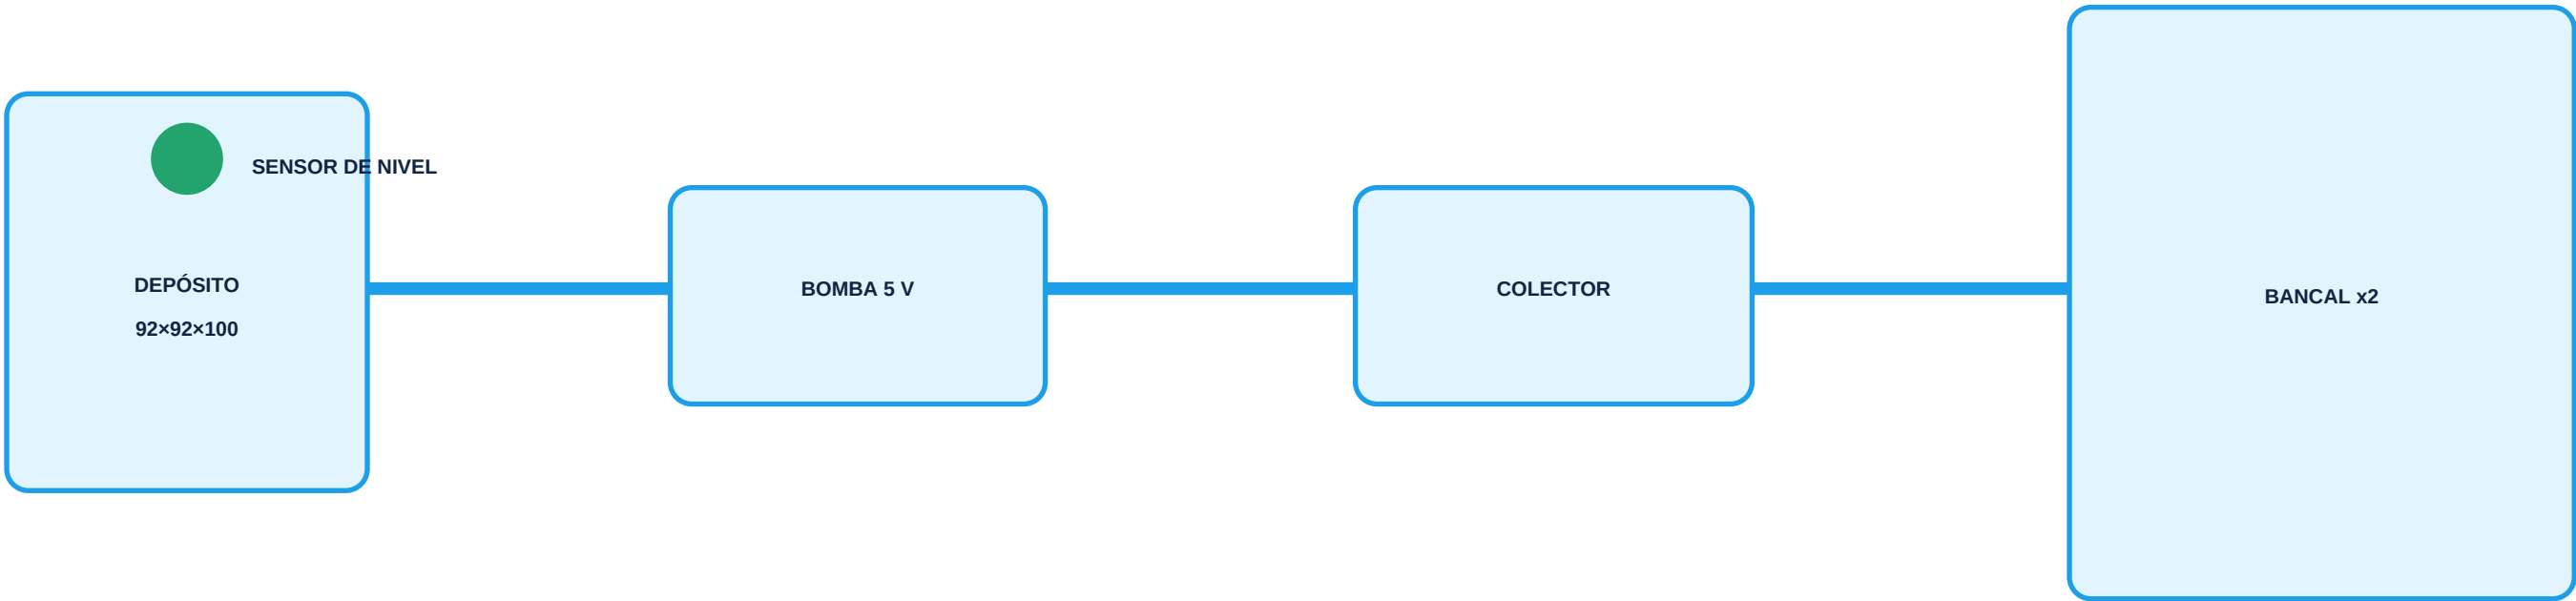

LÓGICA DE PROTECCIÓN

1. Humedad < 30 % → solicitud de riego.


2. Nivel bajo → bomba bloqueada y alarma local.
3. Nivel suficiente → riego hasta 45 %.

4. Tiempo máximo de bomba: 120 s.

Nunca ubicar agua o uniones de manguera sobre el gabinete electrónico.

EXPLOSIÓN, MONTAJE Y CORTE

Secuencia de armado y criterios de tolerancia

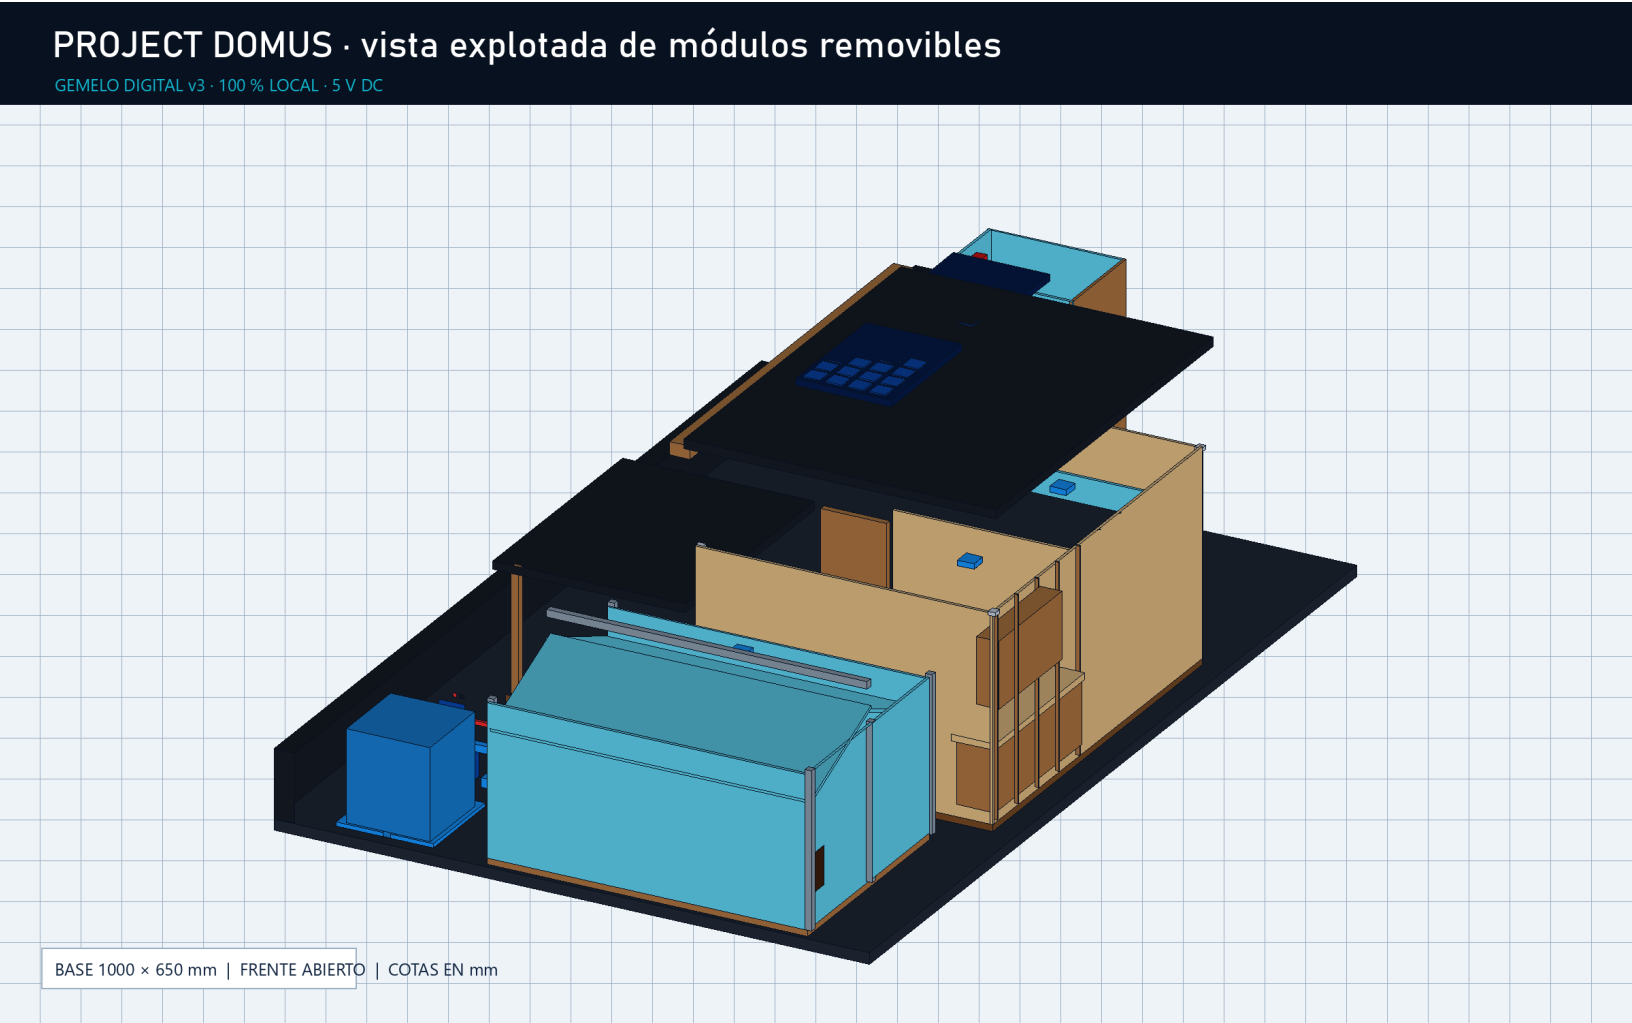

SECUENCIA

- 1 · Nivelar base 1000 × 650.
- 2 · Montar casa y tabiques.
- 3 · Armar porche e invernadero.
- 4 · Separar depósito y gabinete.
- 5 · Tender agua antes de energía.
- 6 · Cablear 5 V/GND y señales.
- 7 · Colocar techo/paneles removibles.
- 8 · Probar bloqueos antes de exhibir.

TOLERANCIA INICIAL ±0.5 mm

Presentar en seco antes de adhesivo definitivo.

BASE	CASA	INVERNADERO	PORCHE	JARVIS	GABINETE
1000×650×12	430×325	250×350×225	250×195×154	105×118×302	110×150×269
Cant. 1	Cant. 1 set	Cant. 1	Cant. 1	Cant. 1	Cant. 1