


PLANOS DE MAQUETA CRUDA

A3 apaisado · sin sensores, conexiones, cableado ni hidráulica instalada

PROJECT DOMUS · maqueta cruda acotada · sin instalaciones

GEMELO DIGITAL v4 · MAQUETA CRUDA · SIN INSTALACIONES

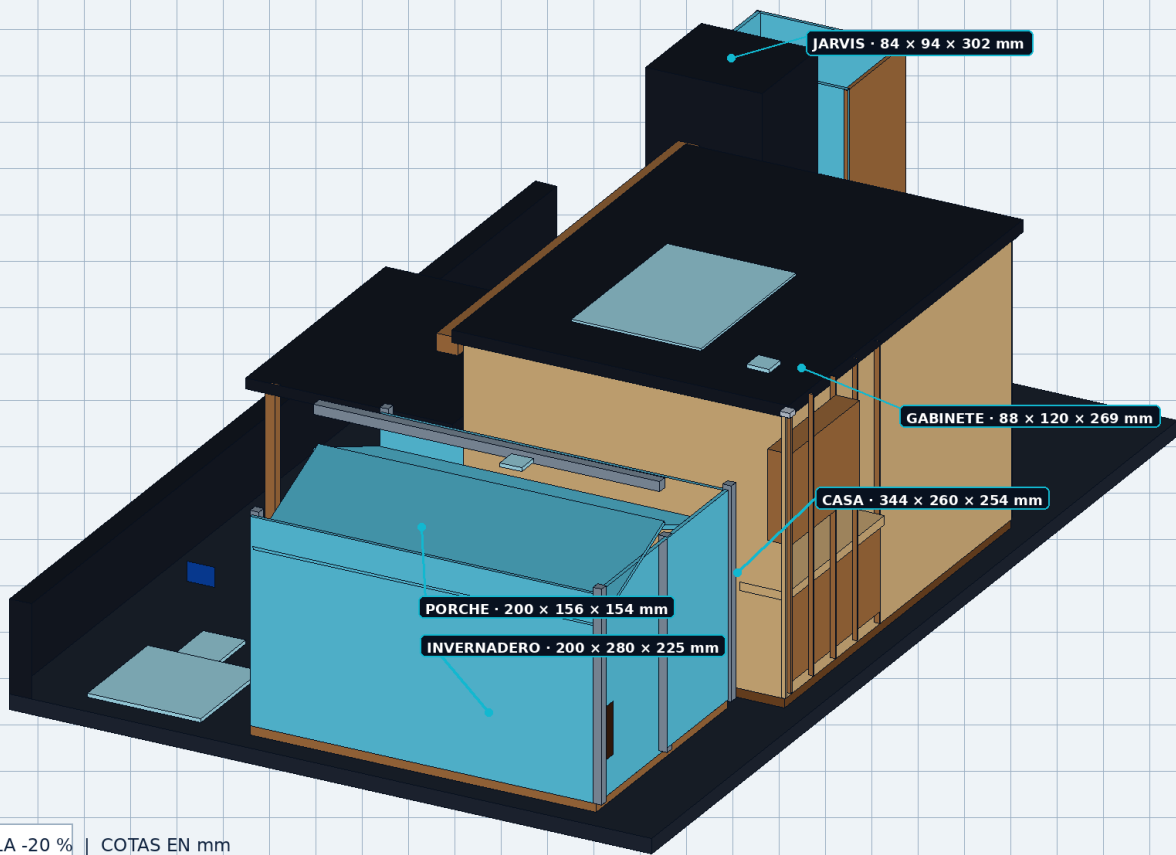

BASE 800 × 520 mm | HUELLA -20 % | COTAS EN mm

ÍNDICE VISUAL


- 01 Implantación y planta general
- 02 Elevaciones y sección
- 03 Reservas técnicas sin instalar
- 04 Carcasas y pasos vacíos
- 05 Explosión, montaje y corte

DATOS PRINCIPALES

Base 800 × 520 × 12 · huella -20 % · estructura sin instalaciones

IMPLANTACIÓN Y PLANTA GENERAL

Ejes, huellas y recorridos principales; el frente de exposición queda abajo

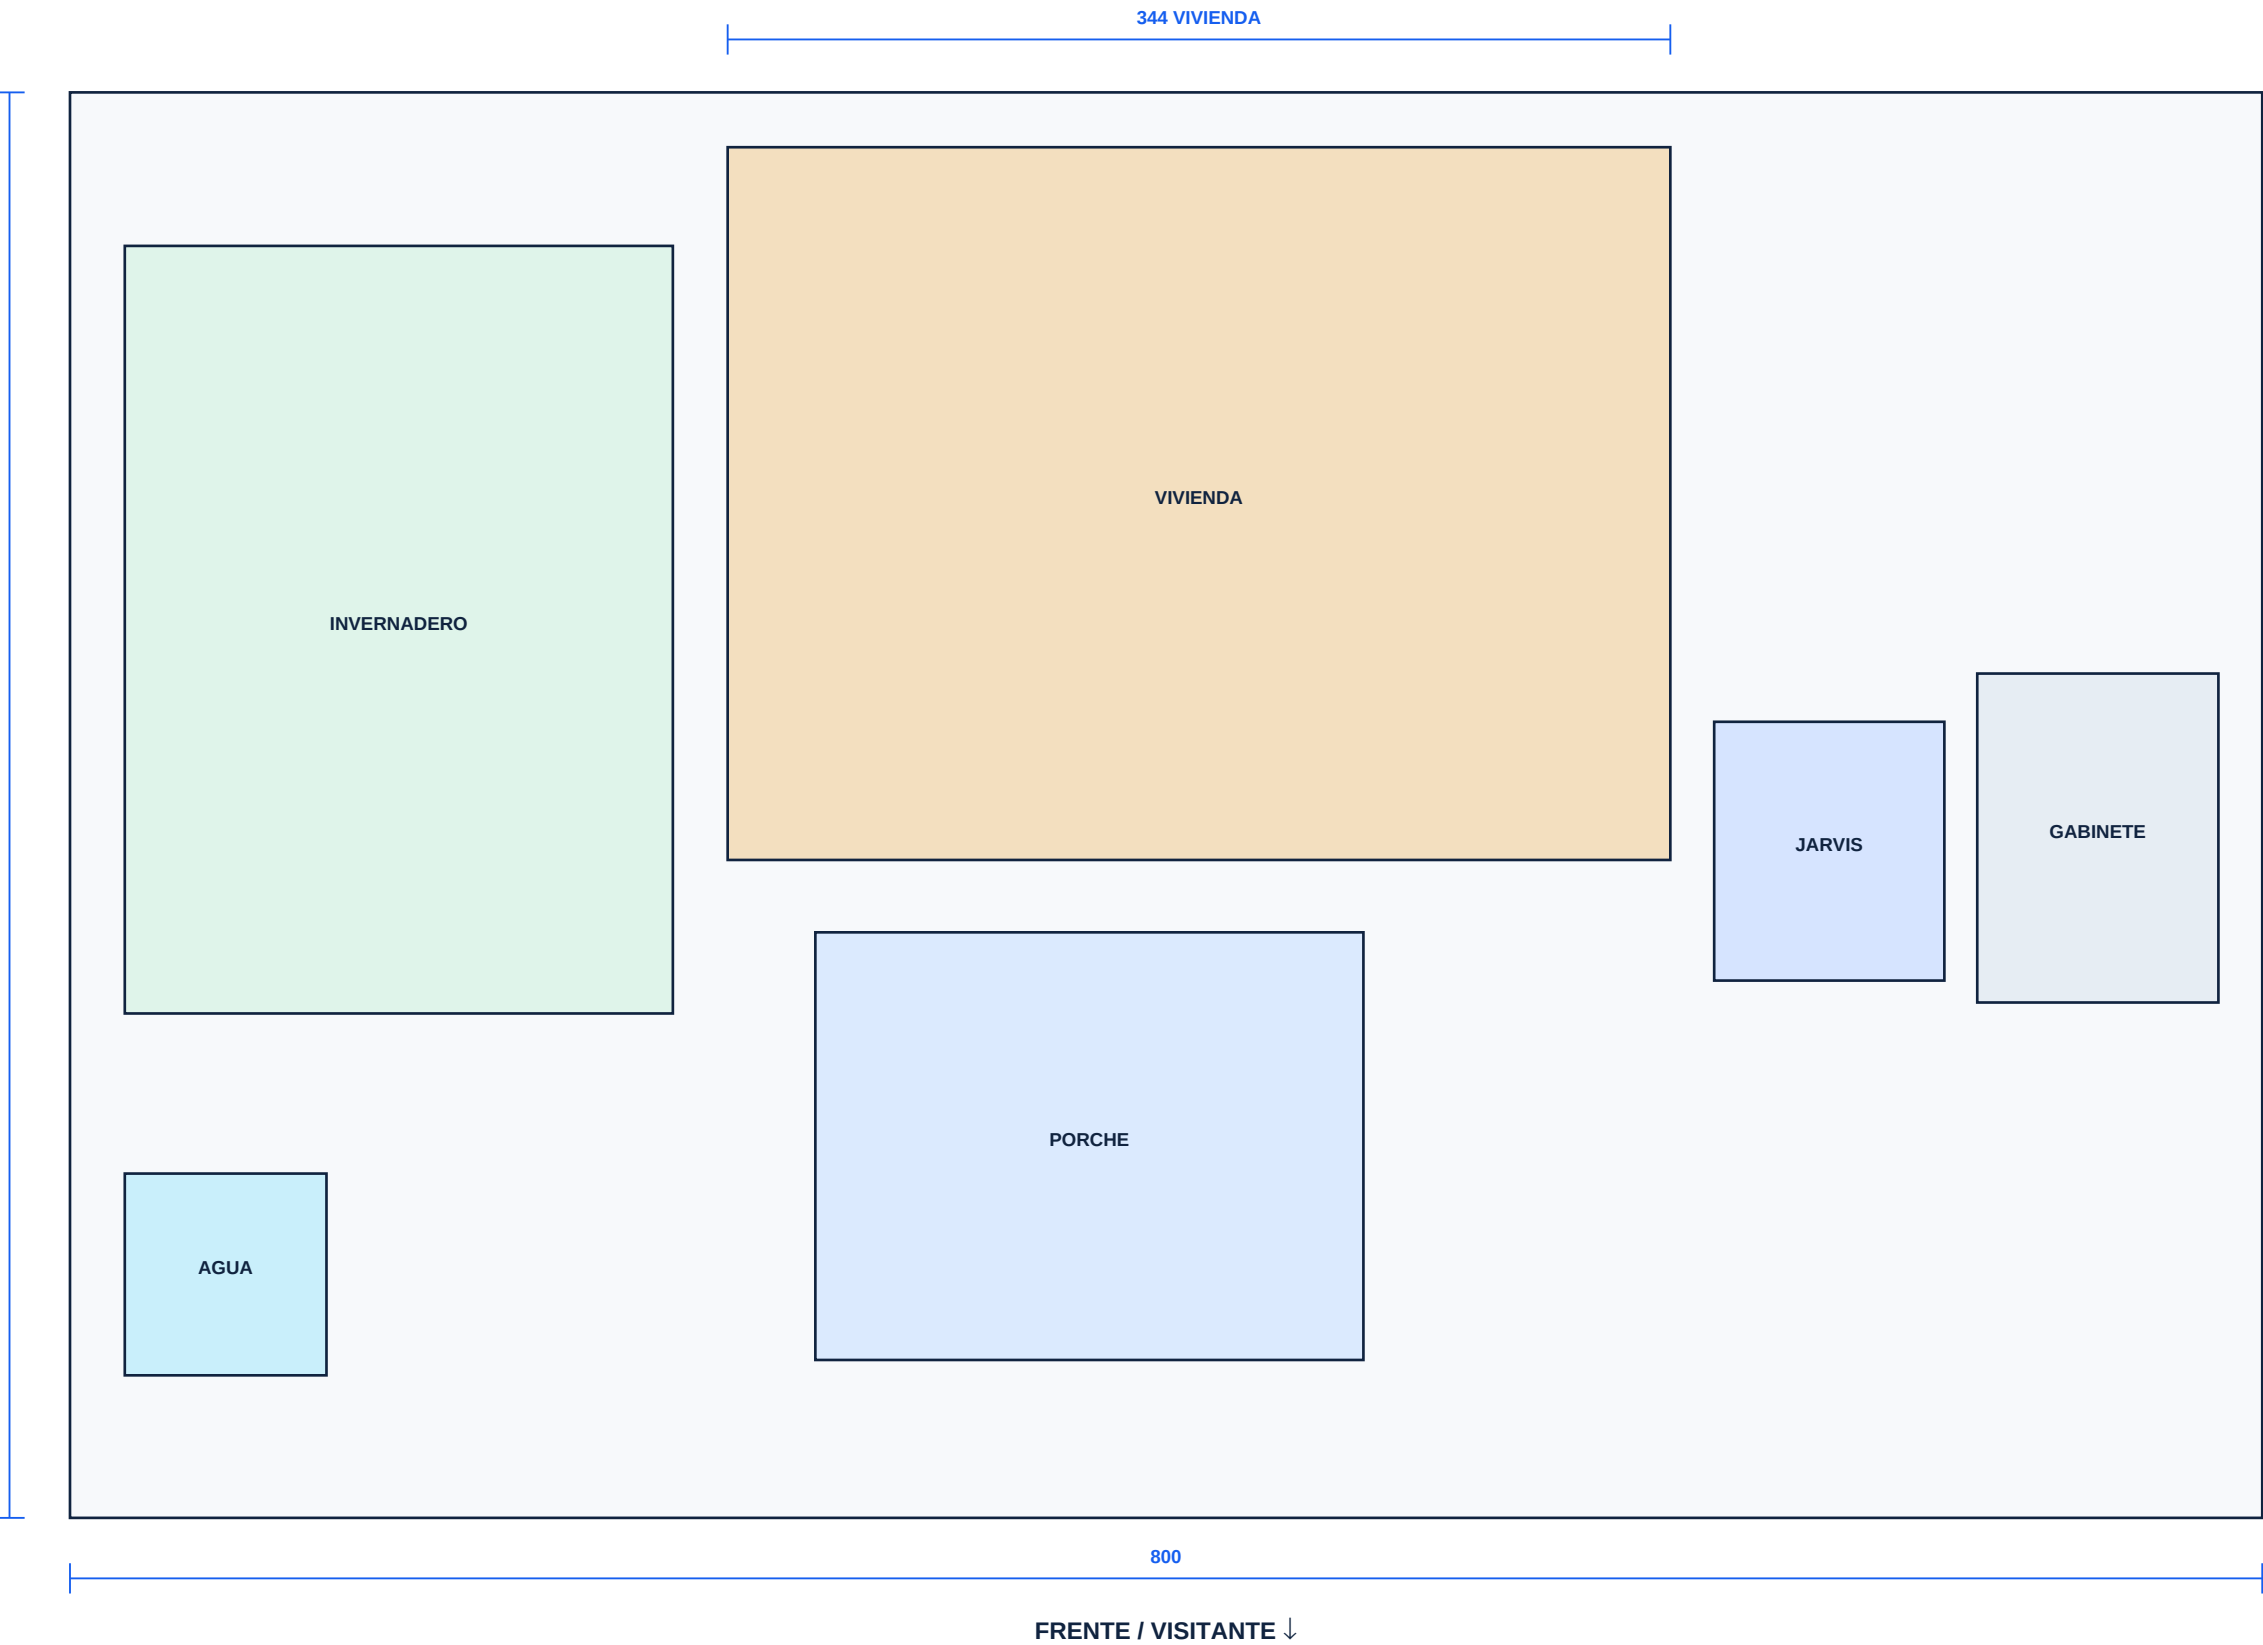

HUELLAS

- Invernadero 200 × 280 × 225
- Casa 344 × 260 × 254 total
- Porche 200 × 156 × 154
- Jarvis 84 × 94 × 302
- Gabinete 88 × 120 × 269
- Depósito real 92 × 92 × 100

ENTREGA DE MAQUETA CRUDA

Sin sensores, placas o conexiones.


Gabinete y Jarvis se entregan vacíos.

Canaleta inferior vacía con tapa.

Techo y frentes permanecen removibles.


ELEVACIONES Y SECCIÓN

Alturas totales y lectura del interior abierto

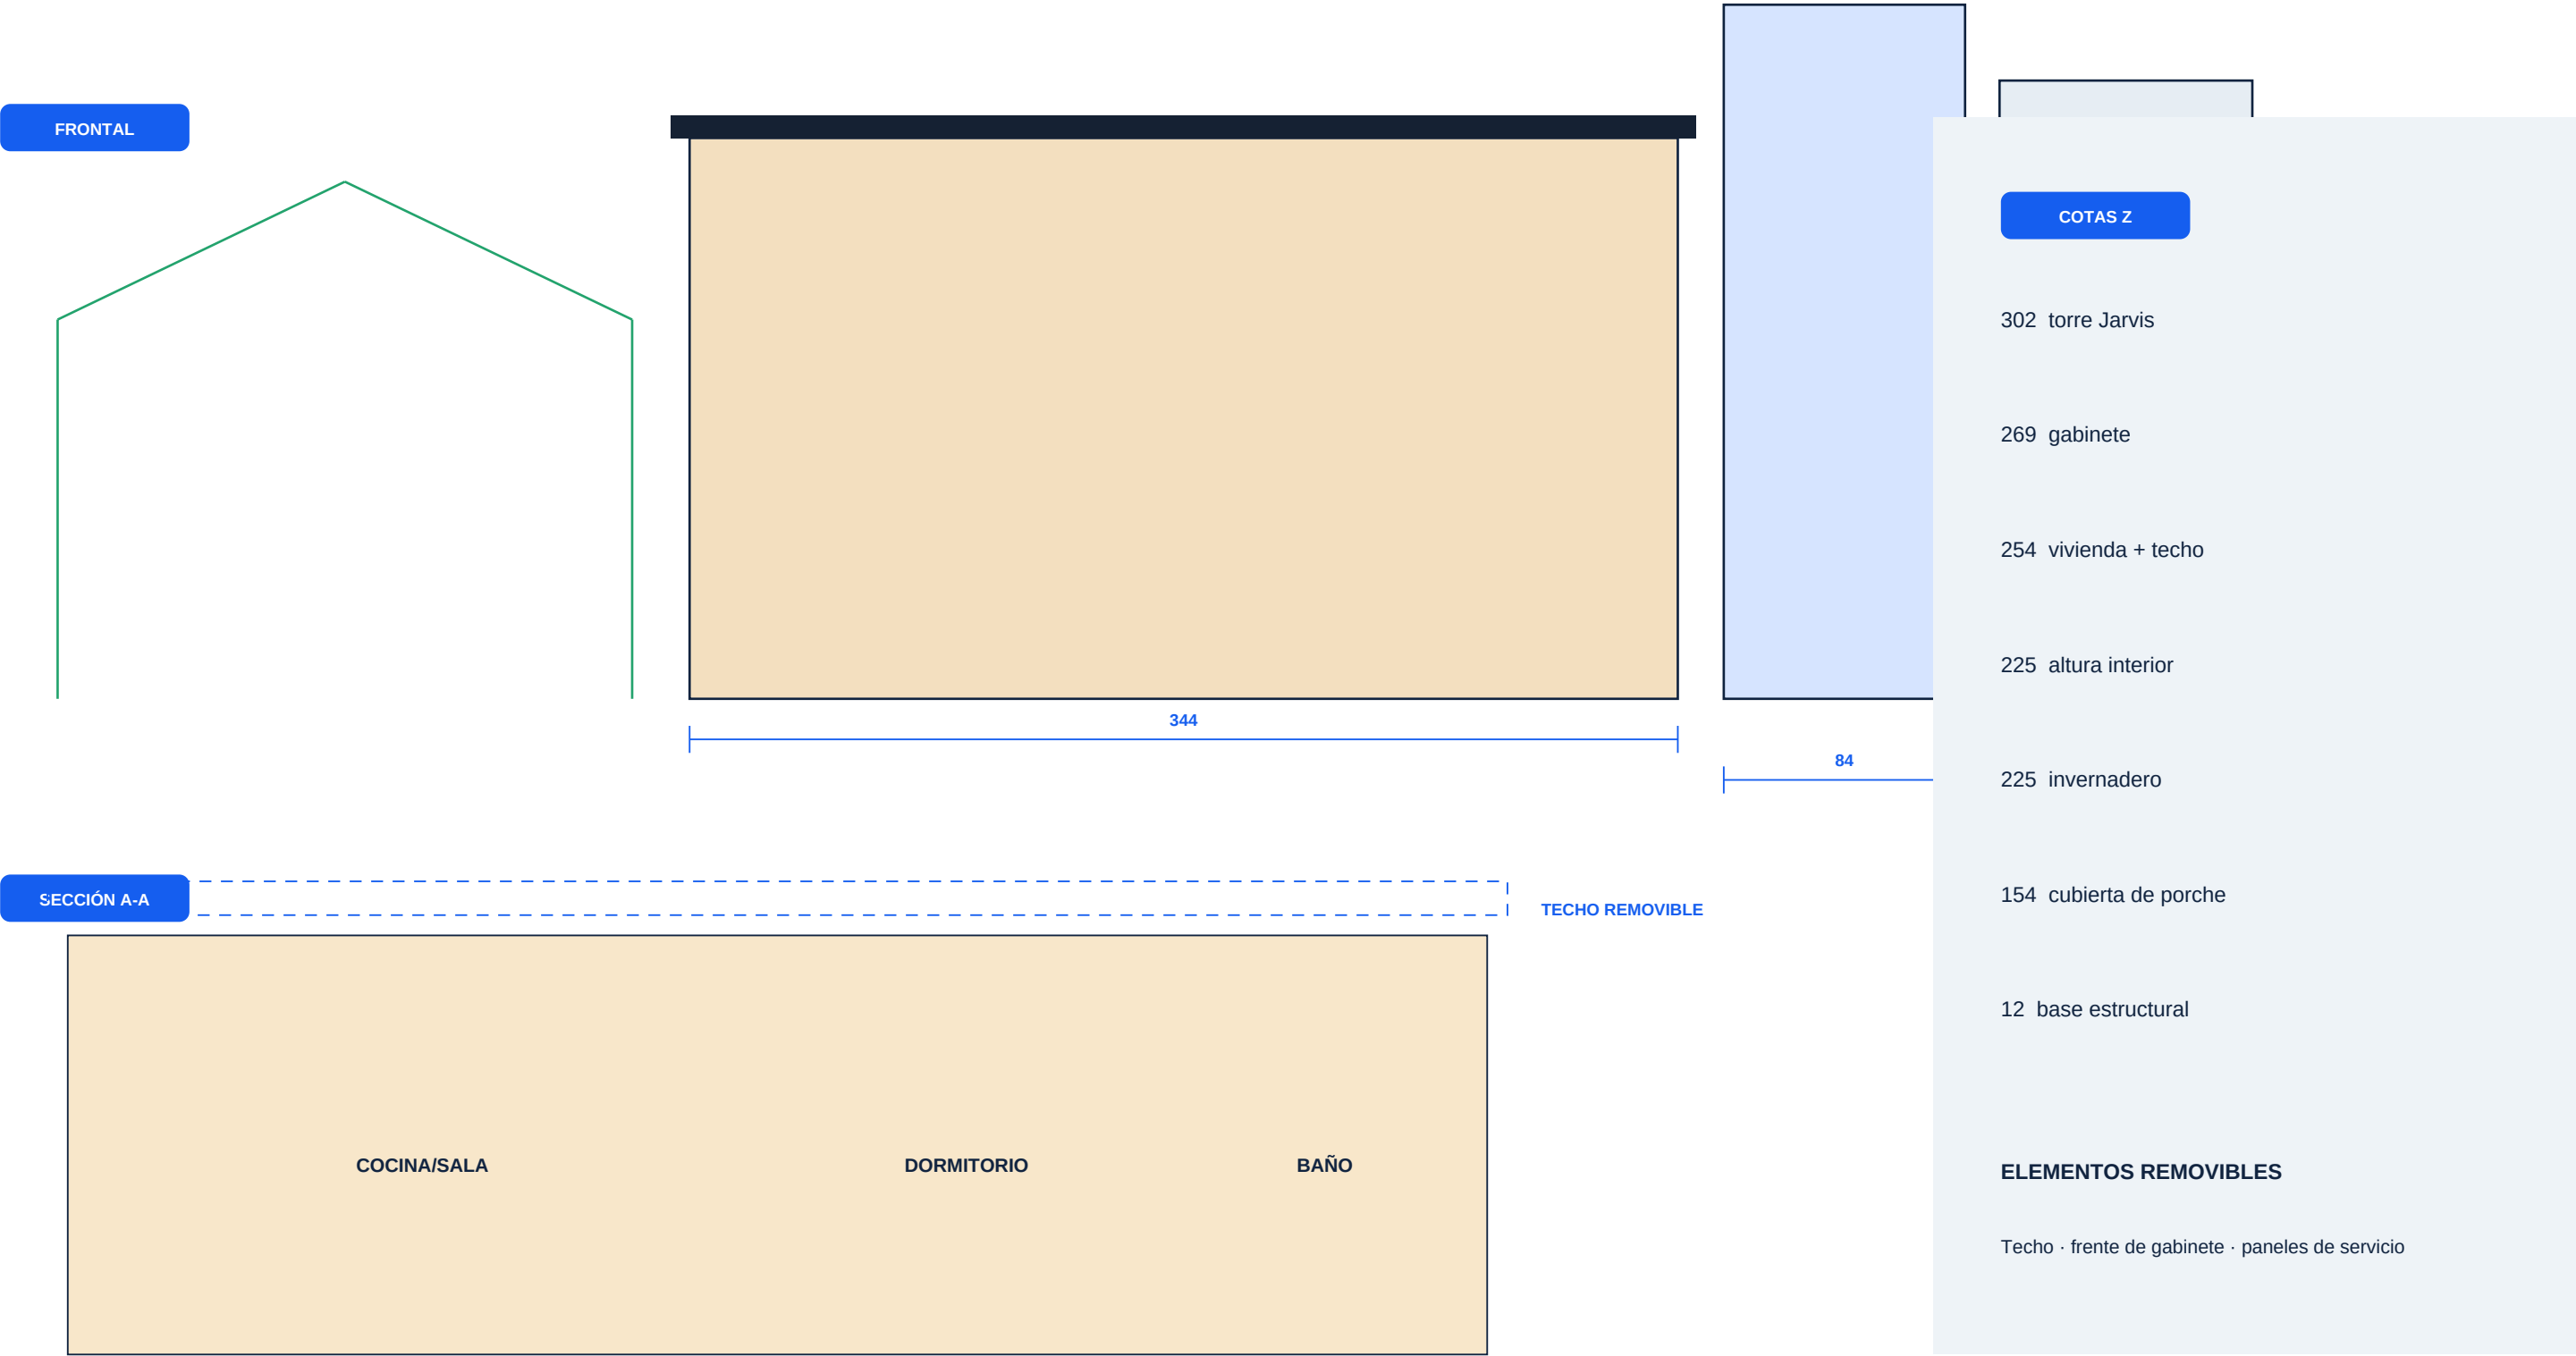

RESERVAS TÉCNICAS · SIN INSTALACIONES

Marcar posiciones; no perforar hasta medir los componentes reales

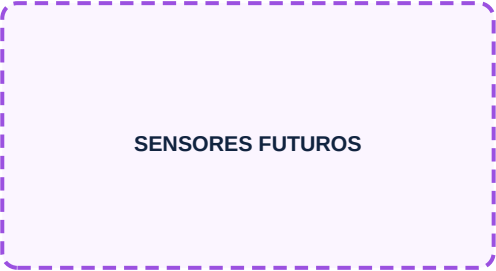

REGLA PARA EL EQUIPO DE ARMADO

Construir las carcasas y marcar reservas con lápiz. No instalar placas, sensores, cables, bomba ni tubería.

CARCASAS Y PASOS VACÍOS

Preparación mecánica para que el circuito se integre después




ENTREGA ESPERADA

1. Estructura firme y escuadrada. 2. Tapas removibles. 3. Reservas marcadas, sin agujeros definitivos.

4. Ninguna conexión, placa, sensor, actuador, manguera o fuente instalada.

EXPLOSIÓN, MONTAJE Y CORTE

Secuencia de armado y criterios de tolerancia

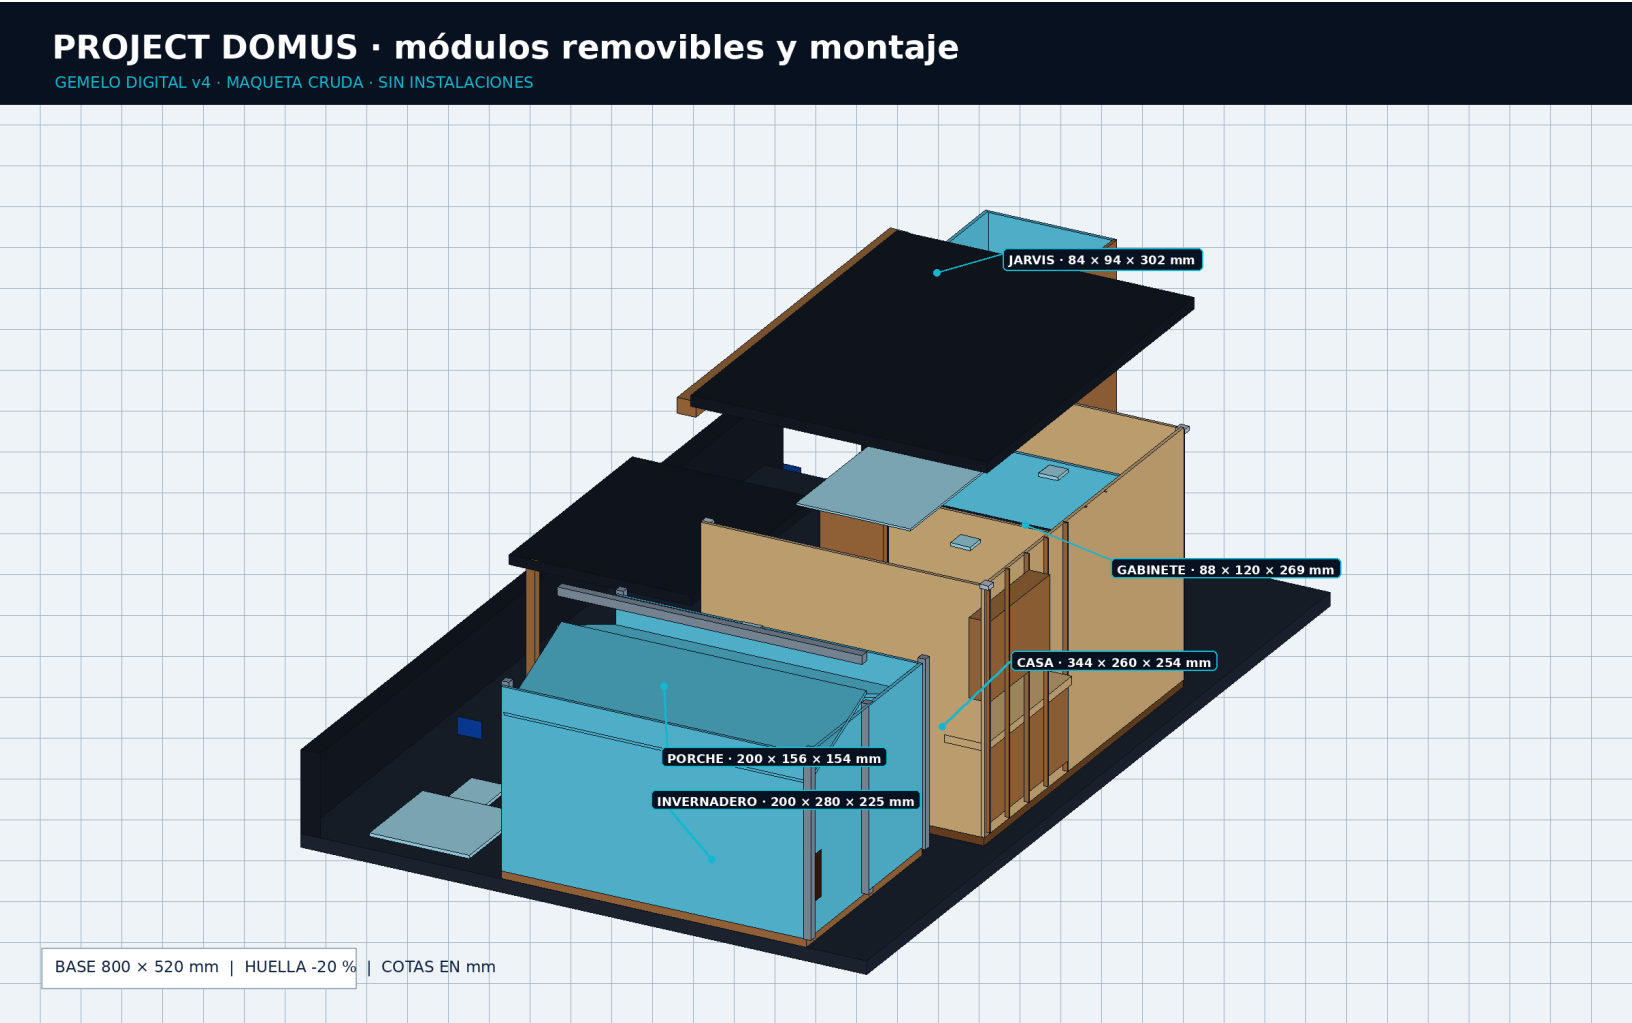

SECUENCIA

- 1 · Nivelar base 800 × 520.
- 2 · Marcar todas las huellas a lápiz.
- 3 · Montar casa y tabiques en seco.
- 4 · Armar porche e invernadero.
- 5 · Construir Jarvis y gabinete vacíos.
- 6 · Colocar canaleta vacía con tapa.
- 7 · Dejar techos y frentes removibles.
- 8 · Entregar sin conexiones ni perforaciones finales.

TOLERANCIA INICIAL ±0.5 mm

Presentar en seco antes de adhesivo definitivo.

BASE	CASA	INVERNADERO	PORCHE	JARVIS	GABINETE
800×520×12	344×260	200×280×225	200×156×154	84×94×302	88×120×269
Cant. 1	Cant. 1 set	Cant. 1	Cant. 1	Cant. 1	Cant. 1